


	1	2	3	4	5	6	7	8	9	10	11	12	13	14	15	16	17	18	
A	DANH SÁCH BẢN VẼ																		A	
B	DỰ ÁN : QUAN TRẮC CHẤT LƯỢNG NƯỚC - NƯỚC SẠCH HUẾ																		B	
	MÔ TẢ : BẢN VẼ LẬP RÁP TỦ ĐIỆN	
	MÃ DỰ ÁN : 1	
C	<table><tr><th rowspan="2">MÃ BẢN VẼ</th><th rowspan="2">TRANG</th><th rowspan="2">MÔ TẢ</th><th colspan="2">LỖI GẦN NHẤT</th></tr><tr><th>NGÀY</th><th>NGƯỜI VẼ</th></tr><tr><td>D</td><td>DWG1-0</td><td>01</td><td>TRANG TRƯỚC</td><td></td><td>CHÂU VƯƠNG PHÁT</td><td></td><td></td><td></td><td></td><td></td><td></td><td></td><td></td><td></td><td></td><td></td><td></td><td></td><td></td></tr><tr><td></td><td>DWG1-1</td><td>02</td><td>DANH SÁCH VẬT TƯ</td><td></td><td>CHÂU VƯƠNG PHÁT</td><td></td><td></td><td></td><td></td><td></td><td></td><td></td><td></td><td></td><td></td><td></td><td></td><td></td><td></td></tr><tr><td></td><td>DWG1-2</td><td>03</td><td>DANH SÁCH VẬT TƯ 2</td><td></td><td>CHÂU VƯƠNG PHÁT</td><td></td><td></td><td></td><td></td><td></td><td></td><td></td><td></td><td></td><td></td><td></td><td></td><td></td><td></td></tr><tr><td>E</td><td>DWG1-3</td><td>04</td><td>BẢNG KÍ HIỆU</td><td></td><td>CHÂU VƯƠNG PHÁT</td><td></td><td></td><td></td><td></td><td></td><td></td><td></td><td></td><td></td><td></td><td></td><td></td><td></td><td></td></tr><tr><td></td><td>DWG1-4</td><td>05</td><td>BẢN VẼ TỦ ĐIỆN</td><td></td><td>CHÂU VƯƠNG PHÁT</td><td></td><td></td><td></td><td></td><td></td><td></td><td></td><td></td><td></td><td></td><td></td><td></td><td></td><td></td></tr><tr><td></td><td>DWG1-5</td><td>06</td><td>BẢN VẼ THÙNG CHỨA MẪU</td><td></td><td>CHÂU VƯƠNG PHÁT</td><td></td><td></td><td></td><td></td><td></td><td></td><td></td><td></td><td></td><td></td><td></td><td></td><td></td><td></td></tr><tr><td>F</td><td>DWG1-6</td><td>07</td><td>BẢN VẼ THIẾT BỊ TỦ</td><td></td><td>CHÂU VƯƠNG PHÁT</td><td></td><td></td><td></td><td></td><td></td><td></td><td></td><td></td><td></td><td></td><td></td><td></td><td></td><td></td></tr><tr><td></td><td>DWG1-7</td><td>08</td><td>SƠ ĐỒ NGUYÊN LÝ</td><td></td><td>CHÂU VƯƠNG PHÁT</td><td></td><td></td><td></td><td></td><td></td><td></td><td></td><td></td><td></td><td></td><td></td><td></td><td></td><td></td></tr><tr><td></td><td>DWG1-8</td><td>09</td><td>KHỞI ĐỘNG NGUỒN</td><td></td><td>CHÂU VƯƠNG PHÁT</td><td></td><td></td><td></td><td></td><td></td><td></td><td></td><td></td><td></td><td></td><td></td><td></td><td></td><td></td></tr><tr><td>G</td><td>DWG1-9</td><td>10</td><td>ĐIỀU KHIỂN BƠM</td><td></td><td>CHÂU VƯƠNG PHÁT</td><td></td><td></td><td></td><td></td><td></td><td></td><td></td><td></td><td></td><td></td><td></td><td></td><td></td><td></td></tr><tr><td></td><td>DWG1-10</td><td>11</td><td>SƠ ĐỒ ĐIỀU KHIỂN</td><td></td><td>CHÂU VƯƠNG PHÁT</td><td></td><td></td><td></td><td></td><td></td><td></td><td></td><td></td><td></td><td></td><td></td><td></td><td></td><td></td></tr><tr><td></td><td>DWG1-11</td><td>12</td><td>SƠ ĐỒ ĐẦU DÂY ĐỀN</td><td></td><td>CHÂU VƯƠNG PHÁT</td><td></td><td></td><td></td><td></td><td></td><td></td><td></td><td></td><td></td><td></td><td></td><td></td><td></td><td></td></tr><tr><td>H</td><td>DWG1-12</td><td>13</td><td>CHẾ ĐỘ TỰ ĐỘNG/ THỦ CÔNG</td><td></td><td>CHÂU VƯƠNG PHÁT</td><td></td><td></td><td></td><td></td><td></td><td></td><td></td><td></td><td></td><td></td><td></td><td></td><td></td><td></td></tr><tr><td></td><td>DWG1-13</td><td>14</td><td>SƠ ĐỒ ĐẦU DÂY CẢM BIẾN</td><td></td><td>CHÂU VƯƠNG PHÁT</td><td></td><td></td><td></td><td></td><td></td><td></td><td></td><td></td><td></td><td></td><td></td><td></td><td></td><td></td></tr><tr><td></td><td>DWG1-14</td><td>15</td><td>SƠ ĐỒ ĐẦU DÂY QUẠT</td><td></td><td>CHÂU VƯƠNG PHÁT</td><td></td><td></td><td></td><td></td><td></td><td></td><td></td><td></td><td></td><td></td><td></td><td></td><td></td><td></td></tr><tr><td></td><td>DWG1-15</td><td>16</td><td>SƠ ĐỒ ĐẦU DÂY BỘ ĐIỀU KHIỂN</td><td></td><td>CHÂU VƯƠNG PHÁT</td><td></td><td></td><td></td><td></td><td></td><td></td><td></td><td></td><td></td><td></td><td></td><td></td><td></td><td></td></tr><tr><td>I</td><td></td><td></td><td></td><td></td><td></td><td></td><td></td><td></td><td></td><td></td><td></td><td></td><td></td><td></td><td></td><td></td><td></td><td></td><td></td></tr><tr><td></td><td></td><td></td><td></td><td></td><td></td><td></td><td></td><td></td><td></td><td></td><td></td><td></td><td></td><td></td><td></td><td></td><td></td><td></td><td></td></tr><tr><td>J</td><td></td><td></td><td></td><td></td><td></td><td></td><td></td><td></td><td></td><td></td><td></td><td></td><td></td><td></td><td></td><td></td><td></td><td></td><td></td></tr><tr><td></td><td></td><td></td><td></td><td></td><td></td><td></td><td></td><td></td><td></td><td></td><td></td><td></td><td></td><td></td><td></td><td></td><td></td><td></td><td></td></tr><tr><td>K</td><td></td><td></td><td></td><td></td><td></td><td></td><td></td><td></td><td></td><td></td><td></td><td></td><td></td><td></td><td></td><td></td><td></td><td></td><td></td></tr><tr><td></td><td></td><td></td><td></td><td></td><td></td><td></td><td></td><td></td><td></td><td></td><td></td><td></td><td></td><td></td><td></td><td></td><td></td><td></td><td></td></tr><tr><td>L</td><td colspan="3">BẢN QUYỀN: THIẾT KẾ VÀ BẢN IN NÀY LÀ TÀI SẢN CỦA CÔNG TY SAIGON VALVE . KHÔNG ĐƯỢC SỬ DỤNG, SAO CHÉP TOÀN BỘ HOẶC MỘT PHẦN NẾU KHÔNG CÓ SỰ CHO PHÉP BẰNG VĂN BẢN CỦA CÔNG TY</td><td colspan="4"> SAIGON VALVE COMPANY LIMITED 124/16-18 Võ Văn Hát, P.Long Trường, TP.Thủ Đức PH : 028 8359 8739 Fax : 0316929581 Website :https://saigonvalve.vn/</td><td colspan="3">DỰ ÁN: QUAN TRẮC CHẤT LƯỢNG NƯỚC - NƯỚC SẠCH HUẾ TIÊU ĐỀ : TRANG TRƯỚC</td><td colspan="2">MÃ BẢN VẼ DWG 1-0</td><td colspan="1">PHIÊN BẢN A</td><td colspan="1">TRANG 01</td><td colspan="1">TỈ LỆ 1/10</td><td colspan="2">DỰ ÁN 1</td></tr><tr><td></td><td colspan="2">NGÀY</td><td colspan="2">NGƯỜI THIẾT KẾ</td><td colspan="2">NGƯỜI KIỂM DUYỆT</td><td colspan="2">NGƯỜI KIỂM DUYỆT</td><td colspan="2"></td><td colspan="2"></td><td colspan="2"></td><td colspan="2"></td><td colspan="2"></td><td colspan="2"></td></tr><tr><td></td><td colspan="2">...</td><td colspan="2">CHÂU VƯƠNG PHÁT</td><td colspan="2">NGUYỄN THÀNH NAM</td><td colspan="2">LÊ VĂN VĨNH</td><td colspan="2"></td><td colspan="2"></td><td colspan="2"></td><td colspan="2"></td><td colspan="2"></td><td colspan="2"></td></tr><tr><td></td><td>1</td><td>2</td><td>3</td><td>4</td><td>5</td><td>6</td><td>7</td><td>8</td><td>9</td><td>10</td><td>11</td><td>12</td><td>13</td><td>14</td><td>15</td><td>16</td><td>17</td><td>18</td><td></td></tr></table>																		MÃ BẢN VẼ	TRANG	MÔ TẢ	LỖI GẦN NHẤT		NGÀY	NGƯỜI VẼ	D	DWG1-0	01	TRANG TRƯỚC		CHÂU VƯƠNG PHÁT																DWG1-1	02	DANH SÁCH VẬT TƯ		CHÂU VƯƠNG PHÁT																DWG1-2	03	DANH SÁCH VẬT TƯ 2		CHÂU VƯƠNG PHÁT															E	DWG1-3	04	BẢNG KÍ HIỆU		CHÂU VƯƠNG PHÁT																DWG1-4	05	BẢN VẼ TỦ ĐIỆN		CHÂU VƯƠNG PHÁT																DWG1-5	06	BẢN VẼ THÙNG CHỨA MẪU		CHÂU VƯƠNG PHÁT															F	DWG1-6	07	BẢN VẼ THIẾT BỊ TỦ		CHÂU VƯƠNG PHÁT																DWG1-7	08	SƠ ĐỒ NGUYÊN LÝ		CHÂU VƯƠNG PHÁT																DWG1-8	09	KHỞI ĐỘNG NGUỒN		CHÂU VƯƠNG PHÁT															G	DWG1-9	10	ĐIỀU KHIỂN BƠM		CHÂU VƯƠNG PHÁT																DWG1-10	11	SƠ ĐỒ ĐIỀU KHIỂN		CHÂU VƯƠNG PHÁT																DWG1-11	12	SƠ ĐỒ ĐẦU DÂY ĐỀN		CHÂU VƯƠNG PHÁT															H	DWG1-12	13	CHẾ ĐỘ TỰ ĐỘNG/ THỦ CÔNG		CHÂU VƯƠNG PHÁT																DWG1-13	14	SƠ ĐỒ ĐẦU DÂY CẢM BIẾN		CHÂU VƯƠNG PHÁT																DWG1-14	15	SƠ ĐỒ ĐẦU DÂY QUẠT		CHÂU VƯƠNG PHÁT																DWG1-15	16	SƠ ĐỒ ĐẦU DÂY BỘ ĐIỀU KHIỂN		CHÂU VƯƠNG PHÁT															I	J	K	L	BẢN QUYỀN: THIẾT KẾ VÀ BẢN IN NÀY LÀ TÀI SẢN CỦA CÔNG TY SAIGON VALVE . KHÔNG ĐƯỢC SỬ DỤNG, SAO CHÉP TOÀN BỘ HOẶC MỘT PHẦN NẾU KHÔNG CÓ SỰ CHO PHÉP BẰNG VĂN BẢN CỦA CÔNG TY			 SAIGON VALVE COMPANY LIMITED 124/16-18 Võ Văn Hát, P.Long Trường, TP.Thủ Đức PH : 028 8359 8739 Fax : 0316929581 Website :https://saigonvalve.vn/				DỰ ÁN: QUAN TRẮC CHẤT LƯỢNG NƯỚC - NƯỚC SẠCH HUẾ TIÊU ĐỀ : TRANG TRƯỚC			MÃ BẢN VẼ DWG 1-0		PHIÊN BẢN A	TRANG 01	TỈ LỆ 1/10	DỰ ÁN 1			NGÀY		NGƯỜI THIẾT KẾ		NGƯỜI KIỂM DUYỆT		NGƯỜI KIỂM DUYỆT															...		CHÂU VƯƠNG PHÁT		NGUYỄN THÀNH NAM		LÊ VĂN VĨNH															1	2	3	4	5	6	7	8	9	10	11	12	13	14	15	16	17	18	
MÃ BẢN VẼ	TRANG	MÔ TẢ	LỖI GẦN NHẤT	
			NGÀY	NGƯỜI VẼ	
D	DWG1-0	01	TRANG TRƯỚC		CHÂU VƯƠNG PHÁT	
	DWG1-1	02	DANH SÁCH VẬT TƯ		CHÂU VƯƠNG PHÁT	
	DWG1-2	03	DANH SÁCH VẬT TƯ 2		CHÂU VƯƠNG PHÁT	
E	DWG1-3	04	BẢNG KÍ HIỆU		CHÂU VƯƠNG PHÁT	
	DWG1-4	05	BẢN VẼ TỦ ĐIỆN		CHÂU VƯƠNG PHÁT	
	DWG1-5	06	BẢN VẼ THÙNG CHỨA MẪU		CHÂU VƯƠNG PHÁT	
F	DWG1-6	07	BẢN VẼ THIẾT BỊ TỦ		CHÂU VƯƠNG PHÁT	
	DWG1-7	08	SƠ ĐỒ NGUYÊN LÝ		CHÂU VƯƠNG PHÁT	
	DWG1-8	09	KHỞI ĐỘNG NGUỒN		CHÂU VƯƠNG PHÁT	
G	DWG1-9	10	ĐIỀU KHIỂN BƠM		CHÂU VƯƠNG PHÁT	
	DWG1-10	11	SƠ ĐỒ ĐIỀU KHIỂN		CHÂU VƯƠNG PHÁT	
	DWG1-11	12	SƠ ĐỒ ĐẦU DÂY ĐỀN		CHÂU VƯƠNG PHÁT	
H	DWG1-12	13	CHẾ ĐỘ TỰ ĐỘNG/ THỦ CÔNG		CHÂU VƯƠNG PHÁT	
	DWG1-13	14	SƠ ĐỒ ĐẦU DÂY CẢM BIẾN		CHÂU VƯƠNG PHÁT	
	DWG1-14	15	SƠ ĐỒ ĐẦU DÂY QUẠT		CHÂU VƯƠNG PHÁT	
	DWG1-15	16	SƠ ĐỒ ĐẦU DÂY BỘ ĐIỀU KHIỂN		CHÂU VƯƠNG PHÁT	
I	
J	
K	
L	BẢN QUYỀN: THIẾT KẾ VÀ BẢN IN NÀY LÀ TÀI SẢN CỦA CÔNG TY SAIGON VALVE . KHÔNG ĐƯỢC SỬ DỤNG, SAO CHÉP TOÀN BỘ HOẶC MỘT PHẦN NẾU KHÔNG CÓ SỰ CHO PHÉP BẰNG VĂN BẢN CỦA CÔNG TY			 SAIGON VALVE COMPANY LIMITED 124/16-18 Võ Văn Hát, P.Long Trường, TP.Thủ Đức PH : 028 8359 8739 Fax : 0316929581 Website :https://saigonvalve.vn/				DỰ ÁN: QUAN TRẮC CHẤT LƯỢNG NƯỚC - NƯỚC SẠCH HUẾ TIÊU ĐỀ : TRANG TRƯỚC			MÃ BẢN VẼ DWG 1-0		PHIÊN BẢN A	TRANG 01	TỈ LỆ 1/10	DỰ ÁN 1	
	NGÀY		NGƯỜI THIẾT KẾ		NGƯỜI KIỂM DUYỆT		NGƯỜI KIỂM DUYỆT	
	...		CHÂU VƯƠNG PHÁT		NGUYỄN THÀNH NAM		LÊ VĂN VĨNH	
	1	2	3	4	5	6	7	8	9	10	11	12	13	14	15	16	17	18	

	1	2	3	4	5	6	7	8	9	10	11	12	13	14	15	16	17	18																			
	STT	KÍ HIỆU	TÊN	MÃ	THÔNG SỐ KỸ THUẬT			NHÀ SẢN XUẤT			SỐ LƯỢNG			GHI CHÚ																							
A	NGUỒN CẤP & MCCB/CB & KHỞI ĐỘNG TỪ																																				
	1	PWS1	Bộ cấp nguồn	EDR-150-24	24VAC/DC			MEANWELL			1																										
	2	PWS2	Bộ cấp nguồn	EDR-120-12	12VAC/DC			MEANWELL			1																										
B	3	MCCB	CB tổng	A9K27225	25A			SCHNEIDER			1																										
	4	CB1	CB	A9F4110	10A			SCHNEIDER			2																										
	5	CB2	CB	A9F4120	20A			SCHNEIDER			1																										
	6	FUSE	Cầu chì 10A 10X38mm	-	10A			-			4																										
C	7	FUSE	Hộp cầu chì	RT18-32	4P - 32A			-			1																										
	8	K1 - K2	Khởi động từ	NCH8-20/20	2P -2NO -20A			CHNT			2																										
	9	SPD	Chống sét	-	-			-			1																										
D	RƠ LE & CẦU ĐẦU NỐI																																				
	10	R1	rơ le 1	MY4NJ-HH54P	24VDC			OMRON			1																										
	11	R2	rơ le 2	MY4NJ-HH54P	24VDC			OMRON			1																										
	12	R3	rơ le 3	MY4NJ-HH54P	24VDC			OMRON			1																										
E	13	R4	rơ le 4	MY4NJ-HH54P	24VDC			OMRON			1																										
	14	R5	rơ le 5	MY4NJ-HH54P	24VDC			OMRON			1																										
	15	R6	rơ le 6	MY4NJ-HH54P	24VDC			OMRON			1																										
	16	TB01	Cầu đầu nối 12P	-	-			-			1																										
F	17	TB02	Cầu đầu nối 12P	-	-			-			1																										
	CONTROL MODULE & MODULE EXPANSION & HMI																																				
	18	TIMER	Đồng hồ điện	KG316T-II	24V ± 15% (AC/DC)			-			1																										
	19	QTCLN	Bộ điều khiển	QTCLN-002	24VDC			SAI GON VALVE			1																										
G	20	HMI	Giao diện người - máy	DOP-107BV	24VDC			DELTA			1																										
	21	FAN	Quạt tủ điện	EA-12038S	24VDC			MASTER			1																										
	22	SENSOR HUB	Bộ điều phối trung tâm	-	12VDC			SAI GON VALVE			1																										
H	SENSORS																																				
	23	SS1	Cảm biến Clo dư	-	DC 9 - 30V						1																										
	24	SS2	Cảm biến Amoni - pH	-	DC 6 - 12V ± 10%						1																										
I	25	SS3	Cảm biến độ đục	DS510	DC 6 - 12V						1																										
	26	-	-	-	-						1																										
	27	WL	Phao nước	-	12VDC			-			1																										
J	LIGHT & SWITCH & MOTOR																																				
	28	PL1	Đỏ	AD16-22D/S	24VAD/DC			-			1																										
	29	PL2	Vàng	AD16-22D/S	24VAC/DC			-			1																										
	30	PL3	Lam	AD16-22D/S	24VAD/DC			-			1																										
K	31	PL4	Lục	AD16-22D/S	24VAC/DC			-			1																										
	32	SW1	Chế độ điều khiển	-	22mm			-			1																										
L	BẢN QUYỀN: THIẾT KẾ VÀ BẢN IN NÀY LÀ TÀI SẢN CỦA CÔNG TY SAIGON VALVE . KHÔNG ĐƯỢC SỬ DỤNG, SAO CHÉP TOÀN BỘ HOẶC MỘT PHẦN NẾU KHÔNG CÓ SỰ CHO PHÉP BẰNG VĂN BẢN CỦA CÔNG TY  SAUGON VALVE COMPANY LIMITED 124/16-18 Võ Văn Hát, P.Long Trường, TP.Thủ Đức PH : 028 8359 8739 Fax : 0316929581 Website :https://saigonvalve.vn/ DỰ ÁN : QUAN TRÁC CHẤT LƯỢNG NƯỚC - NƯỚC SẠCH HUẾ TIÊU ĐỀ DANH SÁCH VẬT TƯ MÃ BẢN VẼ DWG 1-1 NGÀY ... PHIÊN BẢN A NGƯỜI THIẾT KẾ CHÂU VƯƠNG PHÁT TRANG 02 NGƯỜI KIỂM DUYỆT NGUYỄN THÀNH NAM TỈ LỆ 1/10 NGƯỜI PHÊ DUYỆT LÊ VĂN VĨNH DỰ ÁN 1 <tr><td></td><td>1</td><td>2</td><td>3</td><td>4</td><td>5</td><td>6</td><td>7</td><td>8</td><td>9</td><td>10</td><td>11</td><td>12</td><td>13</td><td>14</td><td>15</td><td>16</td><td>17</td><td>18</td></tr>																			1	2	3	4	5	6	7	8	9	10	11	12	13	14	15	16	17	18
	1	2	3	4	5	6	7	8	9	10	11	12	13	14	15	16	17	18																			

	1	2	3	4	5	6	7	8	9	10	11	12	13	14	15	16	17	18
A	STT	KÍ HIỆU	TÊN	MÃ	THÔNG SỐ KỸ THUẬT	NHÀ SẢN XUẤT	SỐ LƯỢNG	GHI CHÚ										
	33	SW2	Điều khiển bơm	LA38	22mm	-	1											
	34	SW3	Điều khiển van 1	LA38	22mm	-	1											
	35	SW4	Điều khiển van 2	LA38	22mm	-	1											
B	36	M1	Bơm 1	-	-	-	1											
	37	M2	Bơm 2	-	-	-	1											
C																		
D																		
E																		
F																		
G																		
H																		
I																		
J																		
K																		
L	BẢN QUYỀN:			SG-VAL  SAUGON VALVE COMPANY LIMITED 124/16-18 Võ Văn Hát, P.Long Trường, TP.Thủ Đức PH : 028 8359 8739 Fax : 0316929581 Website :https://saigonvalve.vn/					DỰ ÁN: QUAN TRÁC CHẤT LƯỢNG NƯỚC - NƯỚC SẠCH HUẾ TIÊU ĐỀ: DANH SÁCH VẬT TƯ 2		MÃ BẢN VẼ DWG 1-2 NGÀY ...		PHIÊN BẢN A NGƯỜI THIẾT KẾ CHÂU VƯƠNG PHÁT	TRANG 03 NGƯỜI KIỂM DUYỆT NGUYỄN THÀNH NAM	TỈ LỆ 1/10 NGƯỜI PHÊ DUYỆT LÊ VĂN VĨNH	DỰ ÁN 1		
	1	2	3	4	5	6	7	8	9	10	11	12	13	14	15	16	17	18

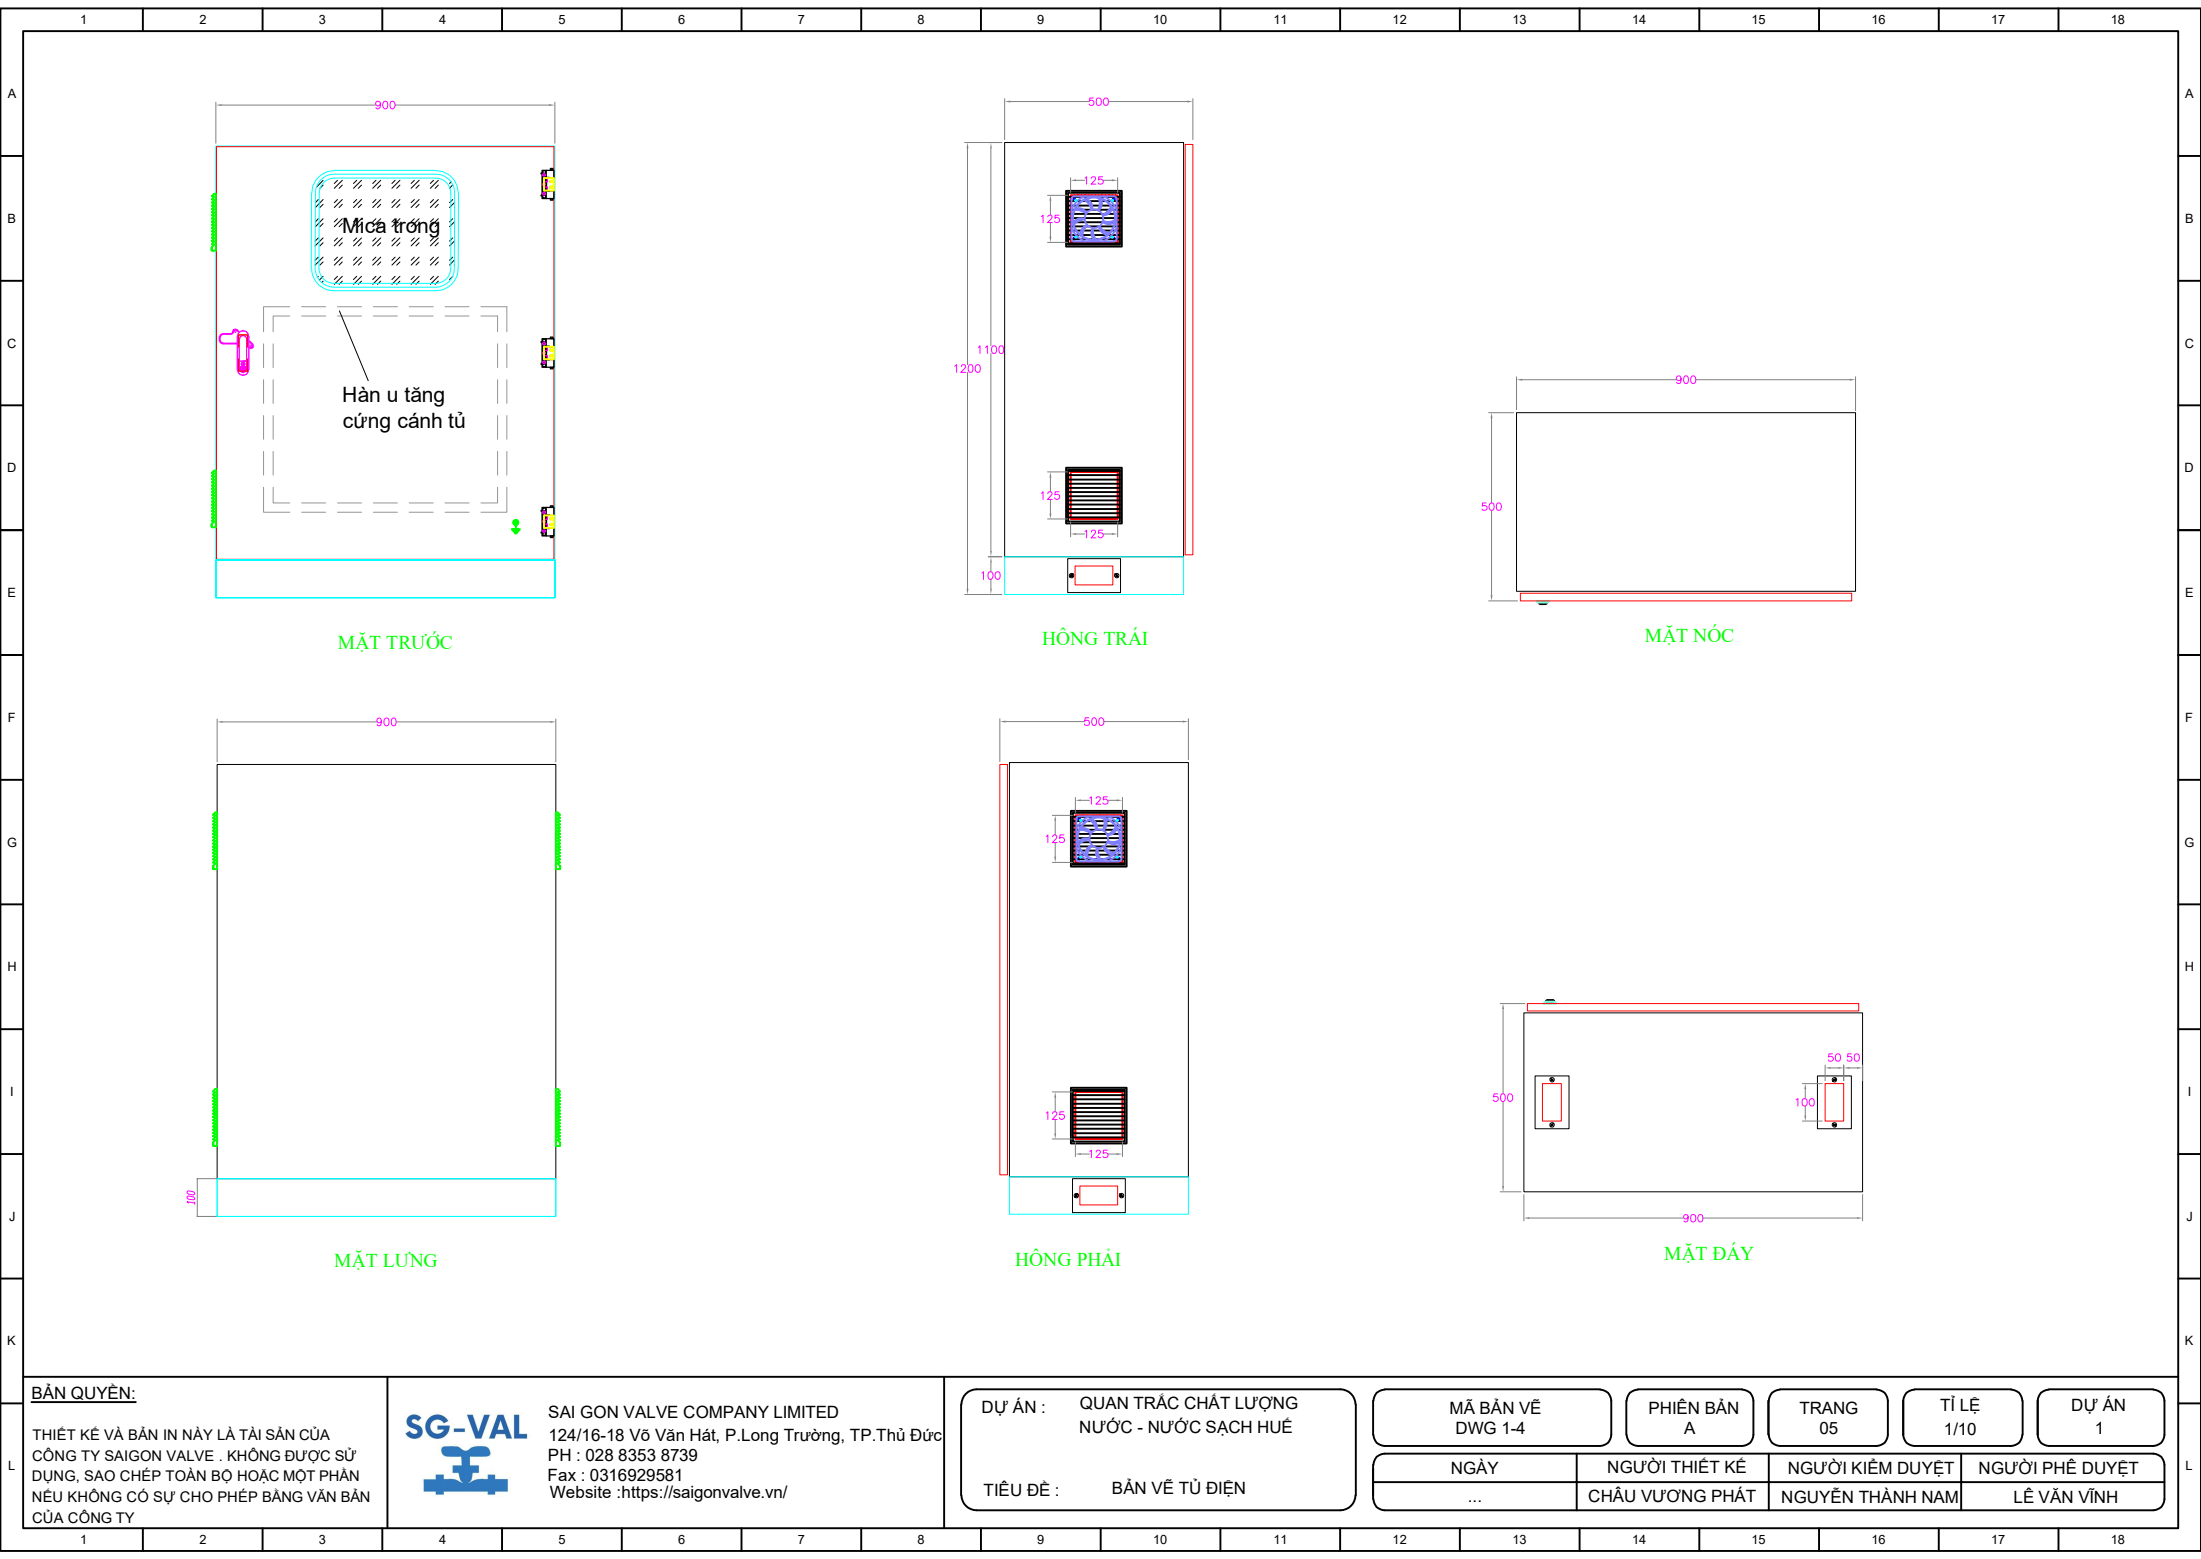

BẢN QUYỀN:

THIẾT KẾ VÀ BẢN IN NÀY LÀ TÀI SẢN CỦA
CÔNG TY SAIGON VALVE . KHÔNG ĐƯỢC SỬ
DỤNG, SAO CHÉP TOÀN BỘ HOẶC MỘT PHẦN
NẾU KHÔNG CÓ SỰ CHO PHÉP BẰNG VĂN BẢN
CỦA CÔNG TY



SAI GON VALVE COMPANY LIMITED
124/16-18 Võ Văn Hát, P.Long Trường, TP.Thủ Đức
PH : 028 8353 8739
Fax : 0316929581
Website : <https://saigonvalve.vn/>

DỰ ÁN : QUAN TRÁC CHẤT LƯỢNG
NƯỚC - NƯỚC SẠCH HUẾ

TIÊU ĐỀ : BẢN VẼ TỦ ĐIỆN

MÃ BẢN VẼ
DWG 1-4

PHIÊN BẢN
A

TRANG
05

TỈ LỆ
1/10

DỰ ÁN
1

NGÀY

NGƯỜI THIẾT KẾ

NGƯỜI KIỂM DUYỆT


NGƯỜI PHÊ DUYỆT

...

CHÂU VƯƠNG PHÁT

NGUYỄN THÀNH NAM

LÊ VĂN VINH

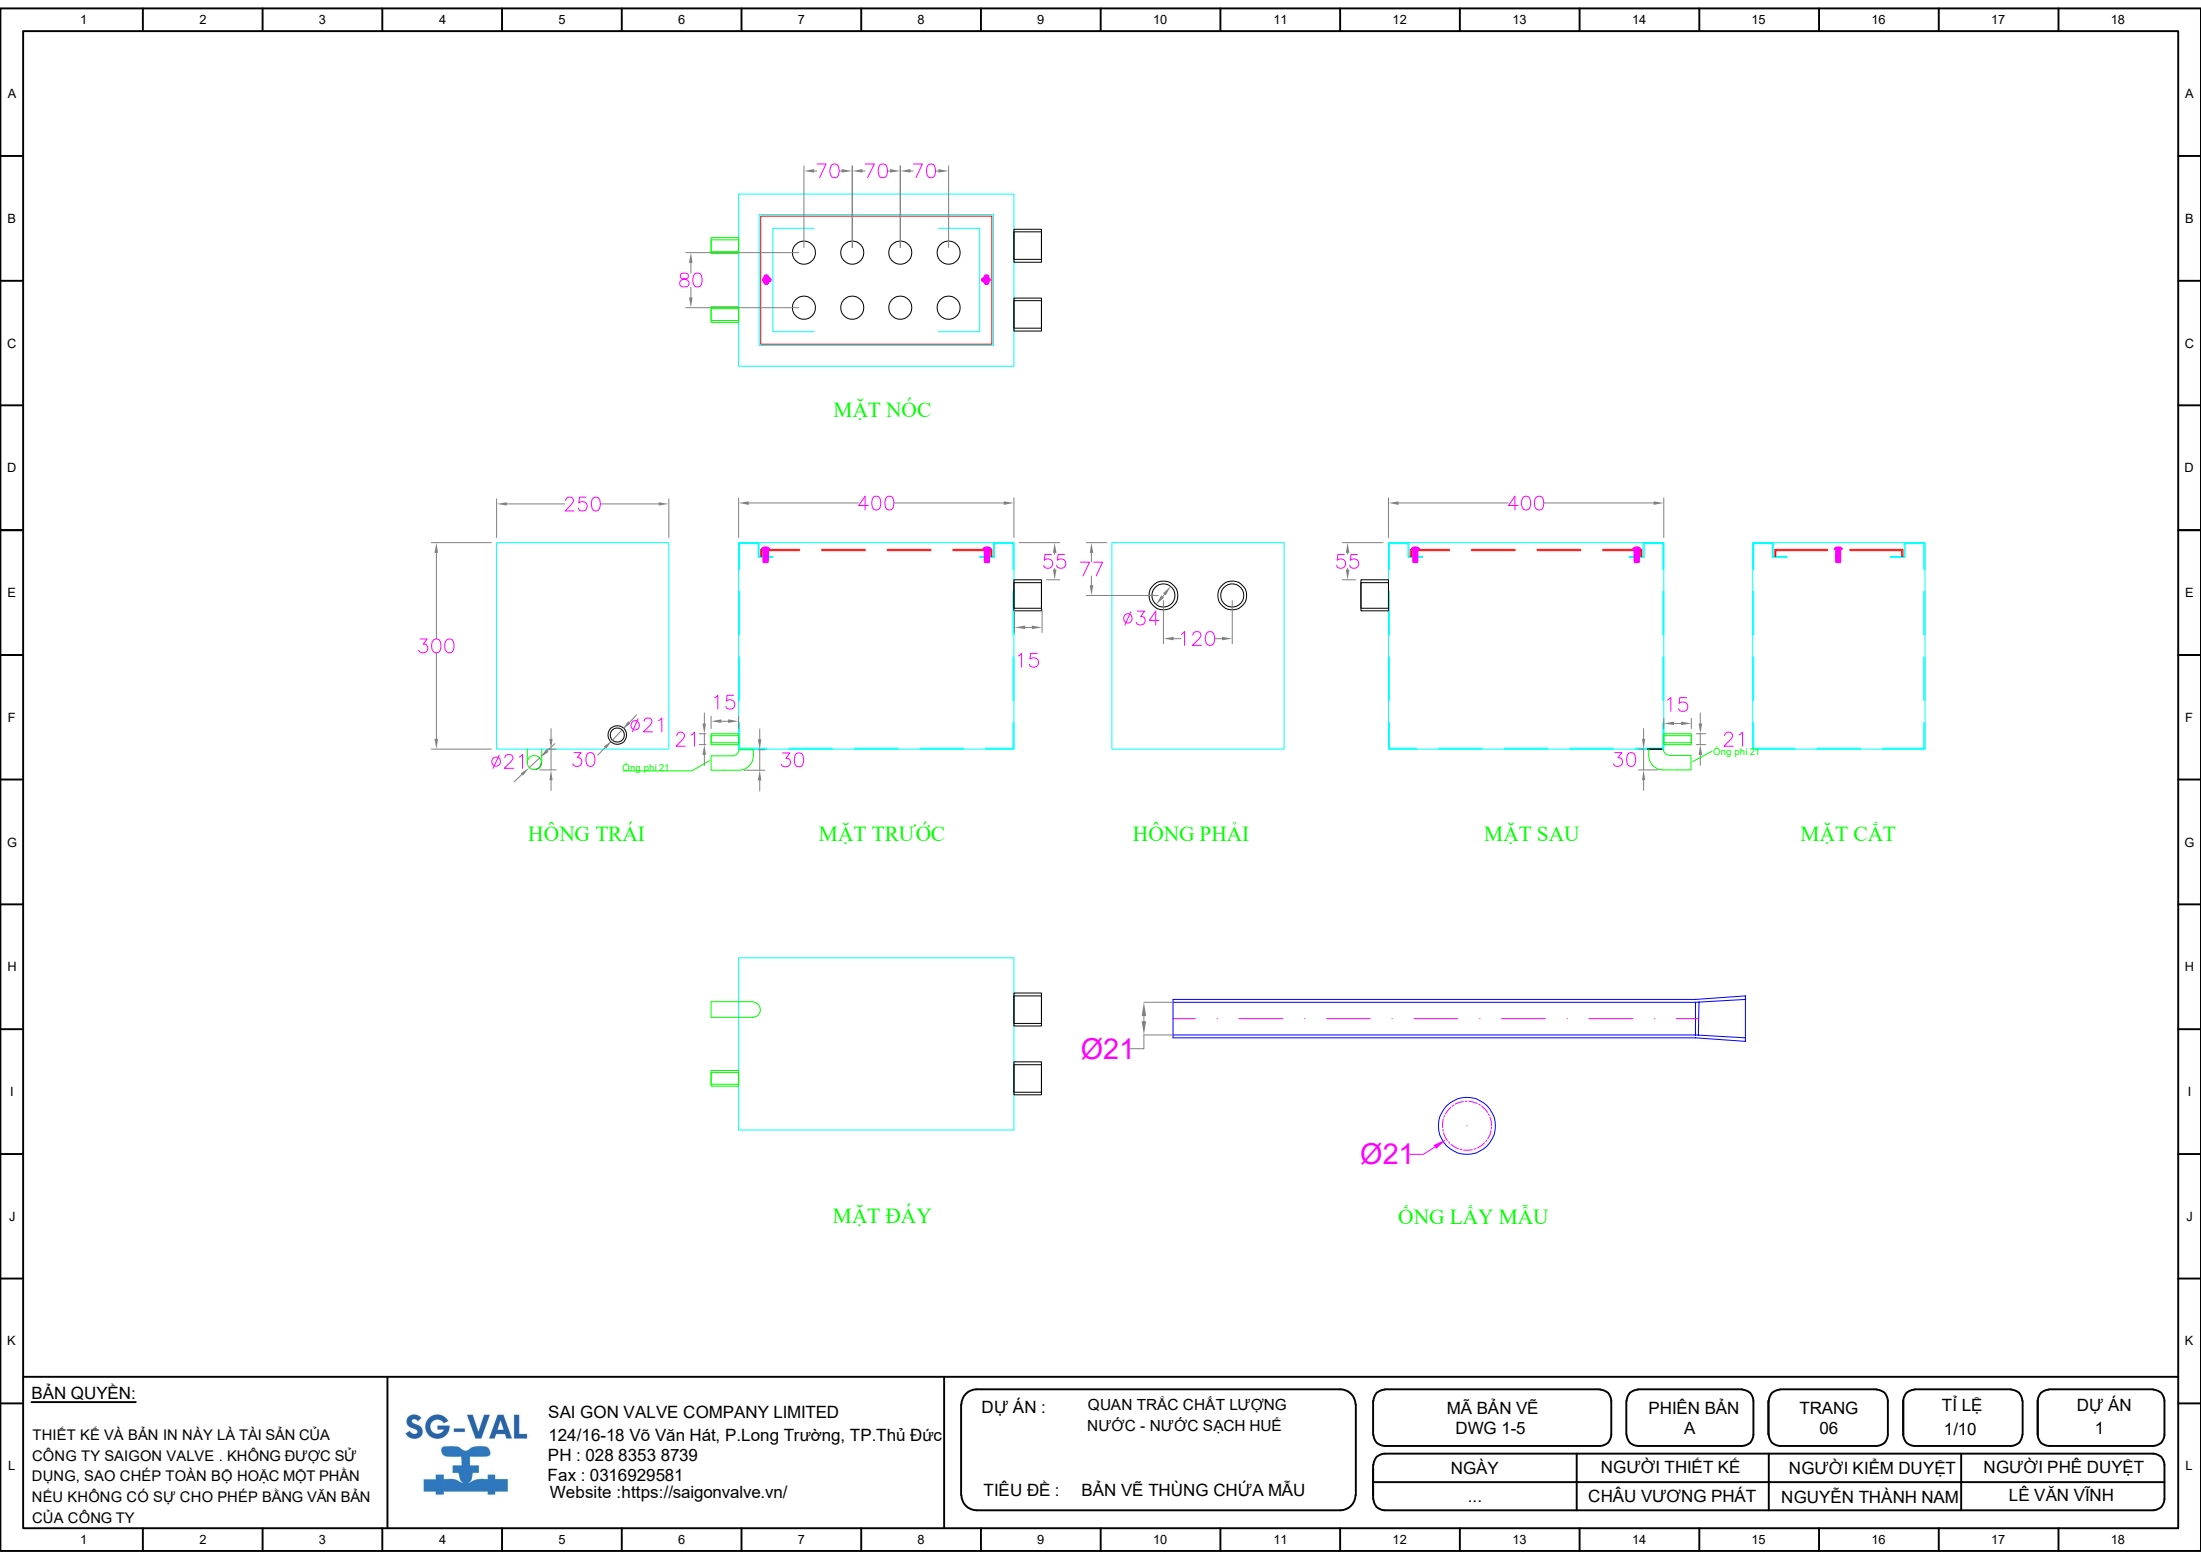

BẢN QUYỀN:

THIẾT KẾ VÀ BẢN IN NÀY LÀ TÀI SẢN CỦA
CÔNG TY SAIGON VALVE . KHÔNG ĐƯỢC SỬ
DỤNG, SAO CHÉP TOÀN BỘ HOẶC MỘT PHẦN
NẾU KHÔNG CÓ SỰ CHO PHÉP BẰNG VĂN BẢN
CỦA CÔNG TY



SAI GON VALVE COMPANY LIMITED
124/16-18 Võ Văn Hát, P.Long Trường, TP.Thủ Đức
PH : 028 8353 8739
Fax : 0316929581
Website : <https://saigonvalve.vn/>

DỰ ÁN : QUAN TRÁC CHẤT LƯỢNG
NƯỚC - NƯỚC SẠCH HUẾ

TIÊU ĐỀ : BẢN VẼ THÙNG CHỨA MẪU

MÃ BẢN VẼ
DWG 1-5

PHIÊN BẢN
A

TRANG
06

TỈ LỆ
1/10

DỰ ÁN
1

NGÀY

NGƯỜI THIẾT KẾ

NGƯỜI KIỂM DUYỆT



NGƯỜI PHÊ DUYỆT

...

CHÂU VƯƠNG PHÁT

NGUYỄN THÀNH NAM

LÊ VĂN VĨNH

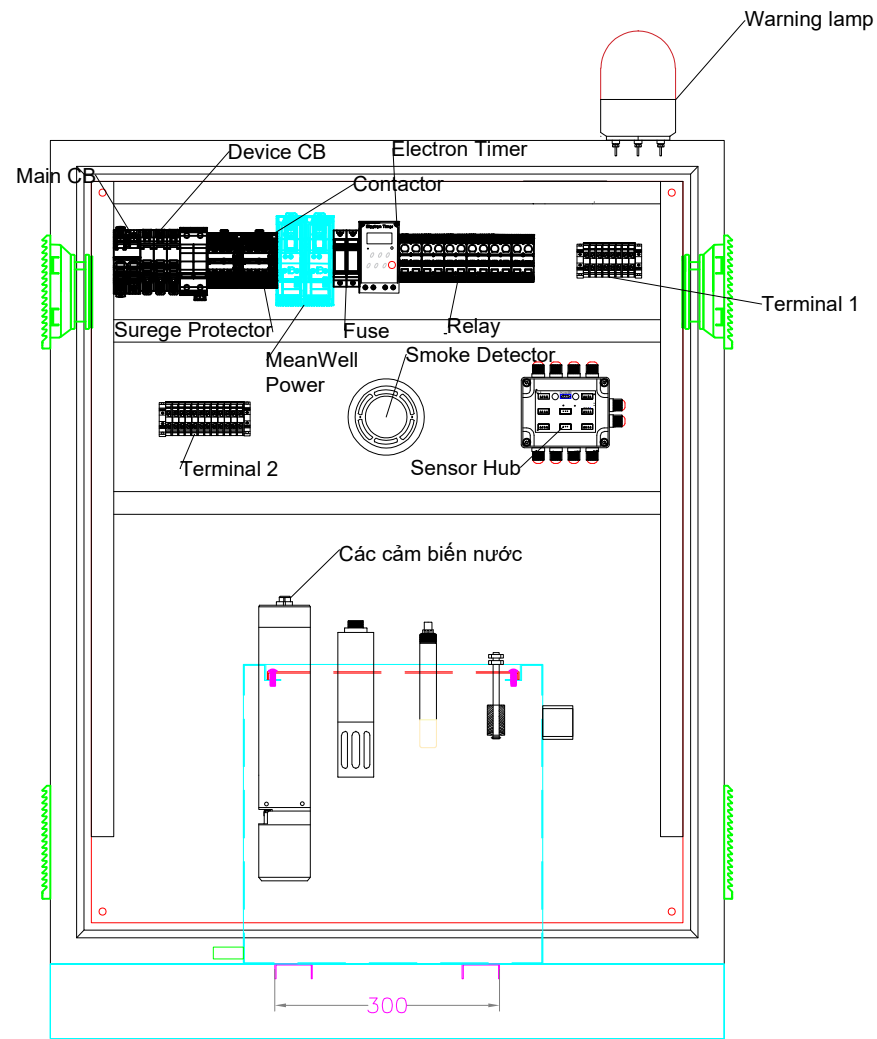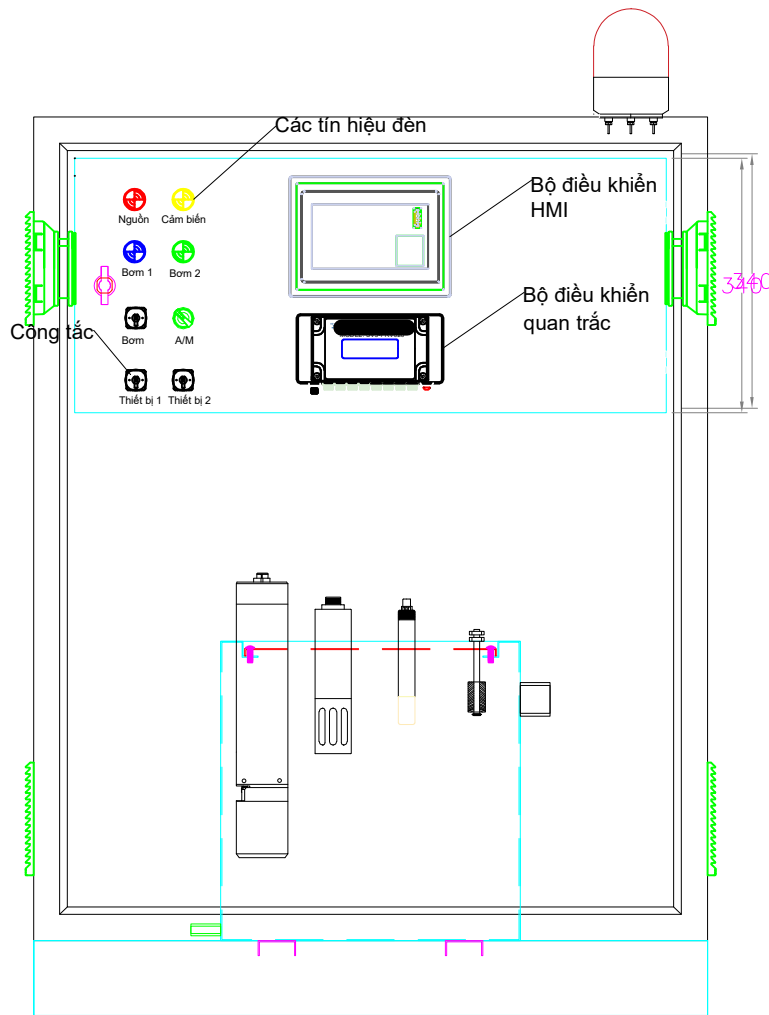

BẢN QUYỀN:

THIẾT KẾ VÀ BẢN IN NÀY LÀ TÀI SẢN CỦA CÔNG TY SAIGON VALVE. KHÔNG ĐƯỢC SỬ DỤNG, SAO CHÉP TOÀN BỘ HOẶC MỘT PHẦN NẾU KHÔNG CÓ SỰ CHO PHÉP BẰNG VĂN BẢN CỦA CÔNG TY



SAIGON VALVE COMPANY LIMITED
124/16-18 Võ Văn Hát, P.Long Trường, TP.Thủ Đức
PH : 028 8353 8739
Fax : 0316929581
Website : <https://saigonvalve.vn/>

DỰ ÁN : QUAN TRẮC CHẤT LƯỢNG NƯỚC - NƯỚC SẠCH HUẾ

TIÊU ĐỀ : BẢN VẼ THIẾT BỊ TỦ

MÃ BẢN VẼ
DWG 1-6

PHIÊN BẢN
A

TRANG
07

TỈ LỆ
1/10


DỰ ÁN
1

NGÀY
...


NGƯỜI THIẾT KẾ
CHÂU VƯƠNG PHÁT

NGƯỜI KIỂM DUYỆT
NGUYỄN THÀNH NAM

NGƯỜI PHÊ DUYỆT
LÊ VĂN VĨNH

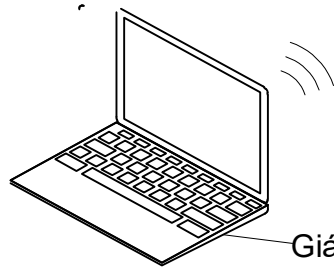


Giám sát và điều khiển
bằng máy tính

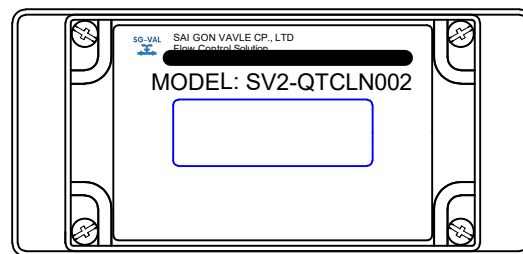

Bộ điều khiển

Giám sát và điều khiển
bằng HMI

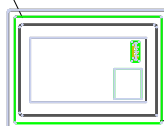

Bộ Hub sensor
Modbus

Bơm nước



Cấp nước cho tủ

WATER
SOURCE

Nguồn nước xả tràn

OUT

BẢN QUYỀN:

THIẾT KẾ VÀ BẢN IN NÀY LÀ TÀI SẢN CỦA
CÔNG TY SAIGON VALVE . KHÔNG ĐƯỢC SỬ
DỤNG, SAO CHÉP TOÀN BỘ HOẶC MỘT PHẦN
NẾU KHÔNG CÓ SỰ CHO PHÉP BẰNG VĂN BẢN
CỦA CÔNG TY



SAIGON VALVE COMPANY LIMITED
124/16-18 Võ Văn Hát, P.Long Trường, TP.Thủ Đức
PH : 028 8353 8739
Fax : 0316929581
Website : <https://saigonvalve.vn/>

DỰ ÁN : QUAN TRẮC CHẤT LƯỢNG
NƯỚC - NƯỚC SẠCH HUẾ

TIÊU ĐỀ : SƠ ĐỒ NGUYÊN LÝ

MÃ BẢN VẼ
DWG 1-7

PHIÊN BẢN
A

TRANG
08

TỈ LỆ
1/10


DỰ ÁN
1

NGÀY
...

NGƯỜI THIẾT KẾ
CHÂU VƯƠNG PHÁT

NGƯỜI KIỂM DUYỆT
NGUYỄN THÀNH NAM

NGƯỜI PHÊ DUYỆT
LÊ VĂN VĨNH

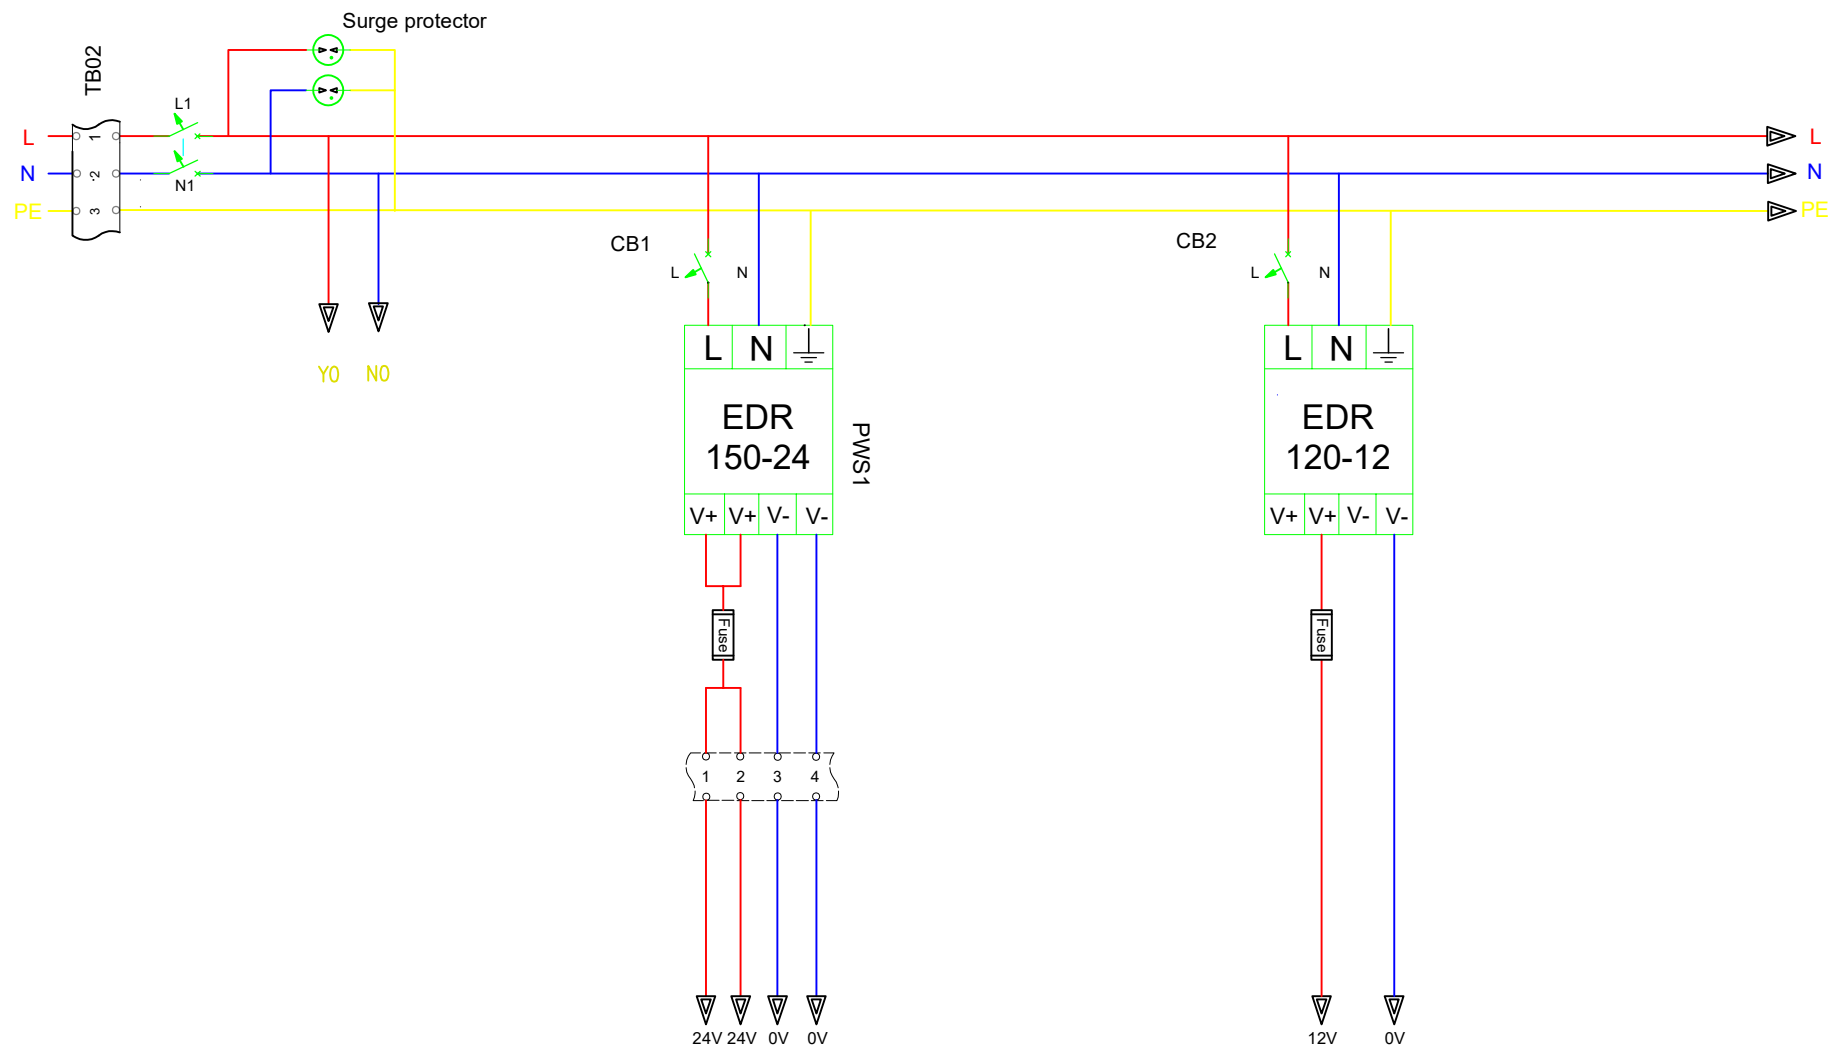

BẢN QUYỀN:

THIẾT KẾ VÀ BẢN IN NÀY LÀ TÀI SẢN CỦA
CÔNG TY SAIGON VALVE . KHÔNG ĐƯỢC SỬ
DỤNG, SAO CHÉP TOÀN BỘ HOẶC MỘT PHẦN
NẾU KHÔNG CÓ SỰ CHO PHÉP BẰNG VĂN BẢN
CỦA CÔNG TY



SAI GON VALVE COMPANY LIMITED
124/16-18 Võ Văn Hát, P.Long Trường, TP.Thủ Đức
PH : 028 8353 8739
Fax : 0316929581
Website : <https://saigonvalve.vn/>

DỰ ÁN : QUAN TRẮC CHẤT LƯỢNG
NƯỚC - NƯỚC SẠCH HUẾ

TIÊU ĐỀ : KHỞI ĐỘNG NGUỒN

MÃ BẢN VẼ
DWG 1-8

PHIÊN BẢN
A

TRANG
09

TỈ LỆ
1/10


DỰ ÁN
1

NGÀY
...

NGƯỜI THIẾT KẾ
CHÂU VƯƠNG PHÁT

NGƯỜI KIỂM DUYỆT
NGUYỄN THÀNH NAM

NGƯỜI PHÊ DUYỆT
LÊ VĂN VINH

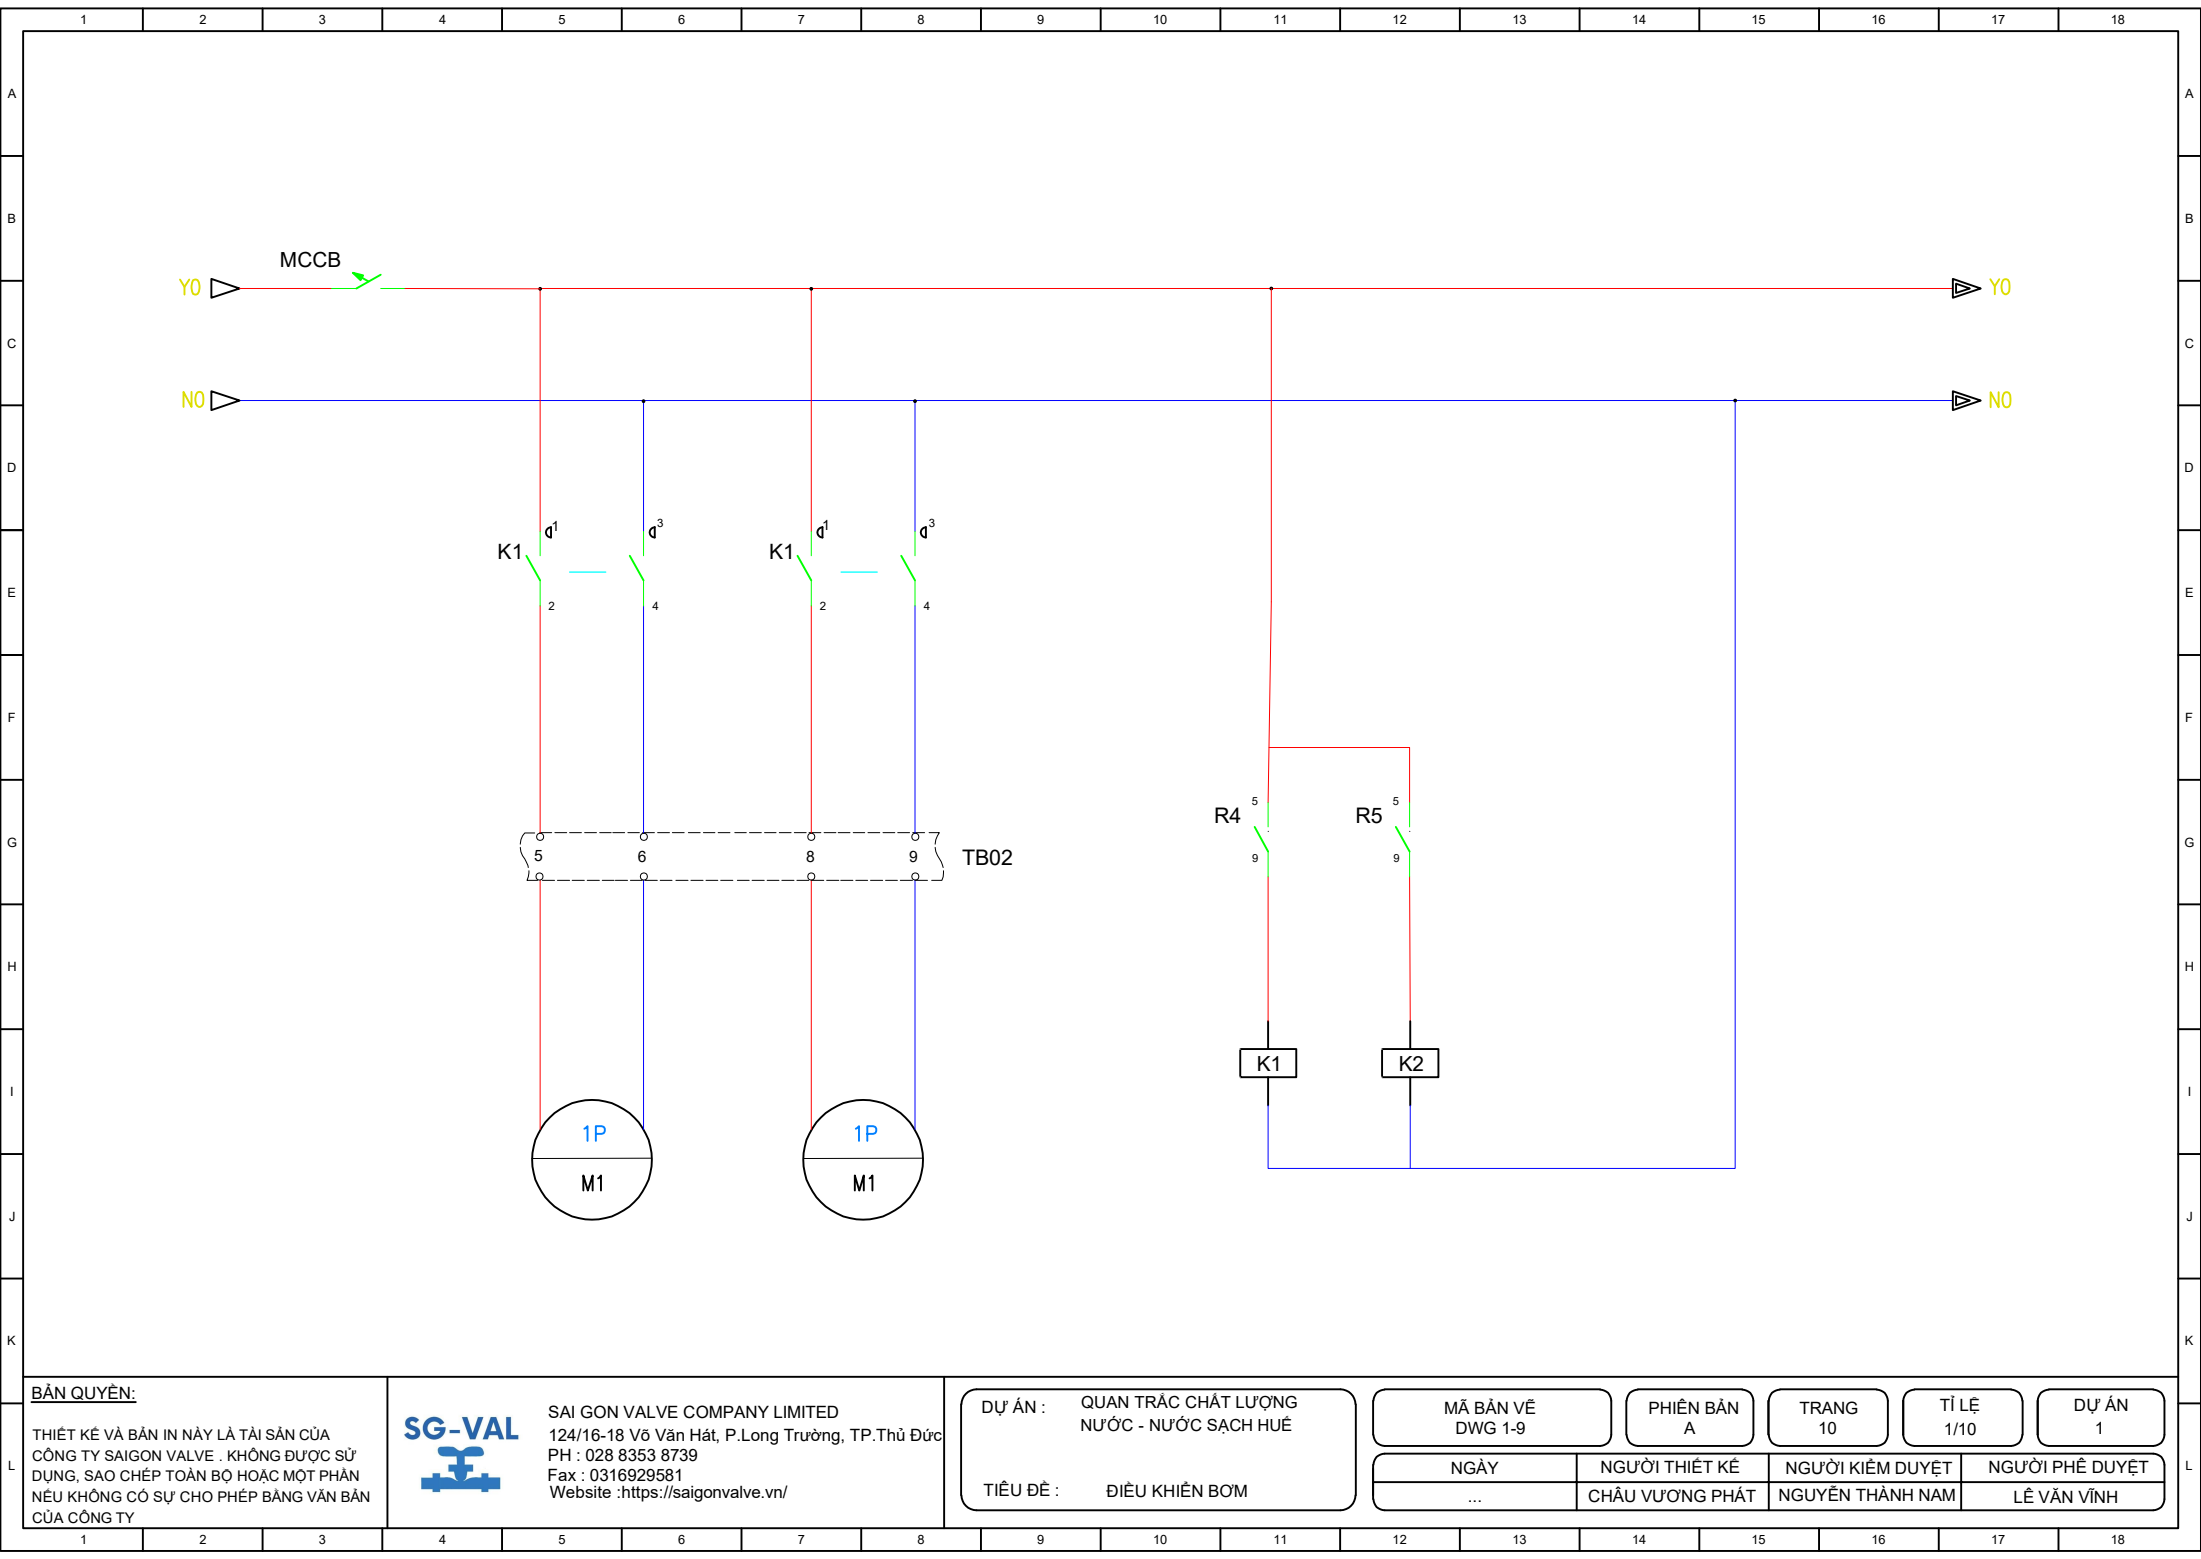

BẢN QUYỀN:

THIẾT KẾ VÀ BẢN IN NÀY LÀ TÀI SẢN CỦA
CÔNG TY SAIGON VALVE . KHÔNG ĐƯỢC SỬ
DỤNG, SAO CHÉP TOÀN BỘ HOẶC MỘT PHẦN
NẾU KHÔNG CÓ SỰ CHO PHÉP BẰNG VĂN BẢN
CỦA CÔNG TY



SAI GON VALVE COMPANY LIMITED
124/16-18 Võ Văn Hát, P.Long Trường, TP.Thủ Đức
PH : 028 8353 8739
Fax : 0316929581
Website : <https://saigonvalve.vn/>

DỰ ÁN : QUAN TRÁC CHẤT LƯỢNG
NƯỚC - NƯỚC SẠCH HUẾ

TIÊU ĐỀ : ĐIỀU KHIỂN BƠM

MÃ BẢN VẼ
DWG 1-9

PHIÊN BẢN
A

TRANG
10

TỈ LỆ
1/10

DỰ ÁN
1

NGÀY

NGƯỜI THIẾT KẾ

NGƯỜI KIỂM DUYỆT


NGƯỜI PHÊ DUYỆT

...

CHÂU VƯƠNG PHÁT

NGUYỄN THÀNH NAM

LÊ VĂN VINH

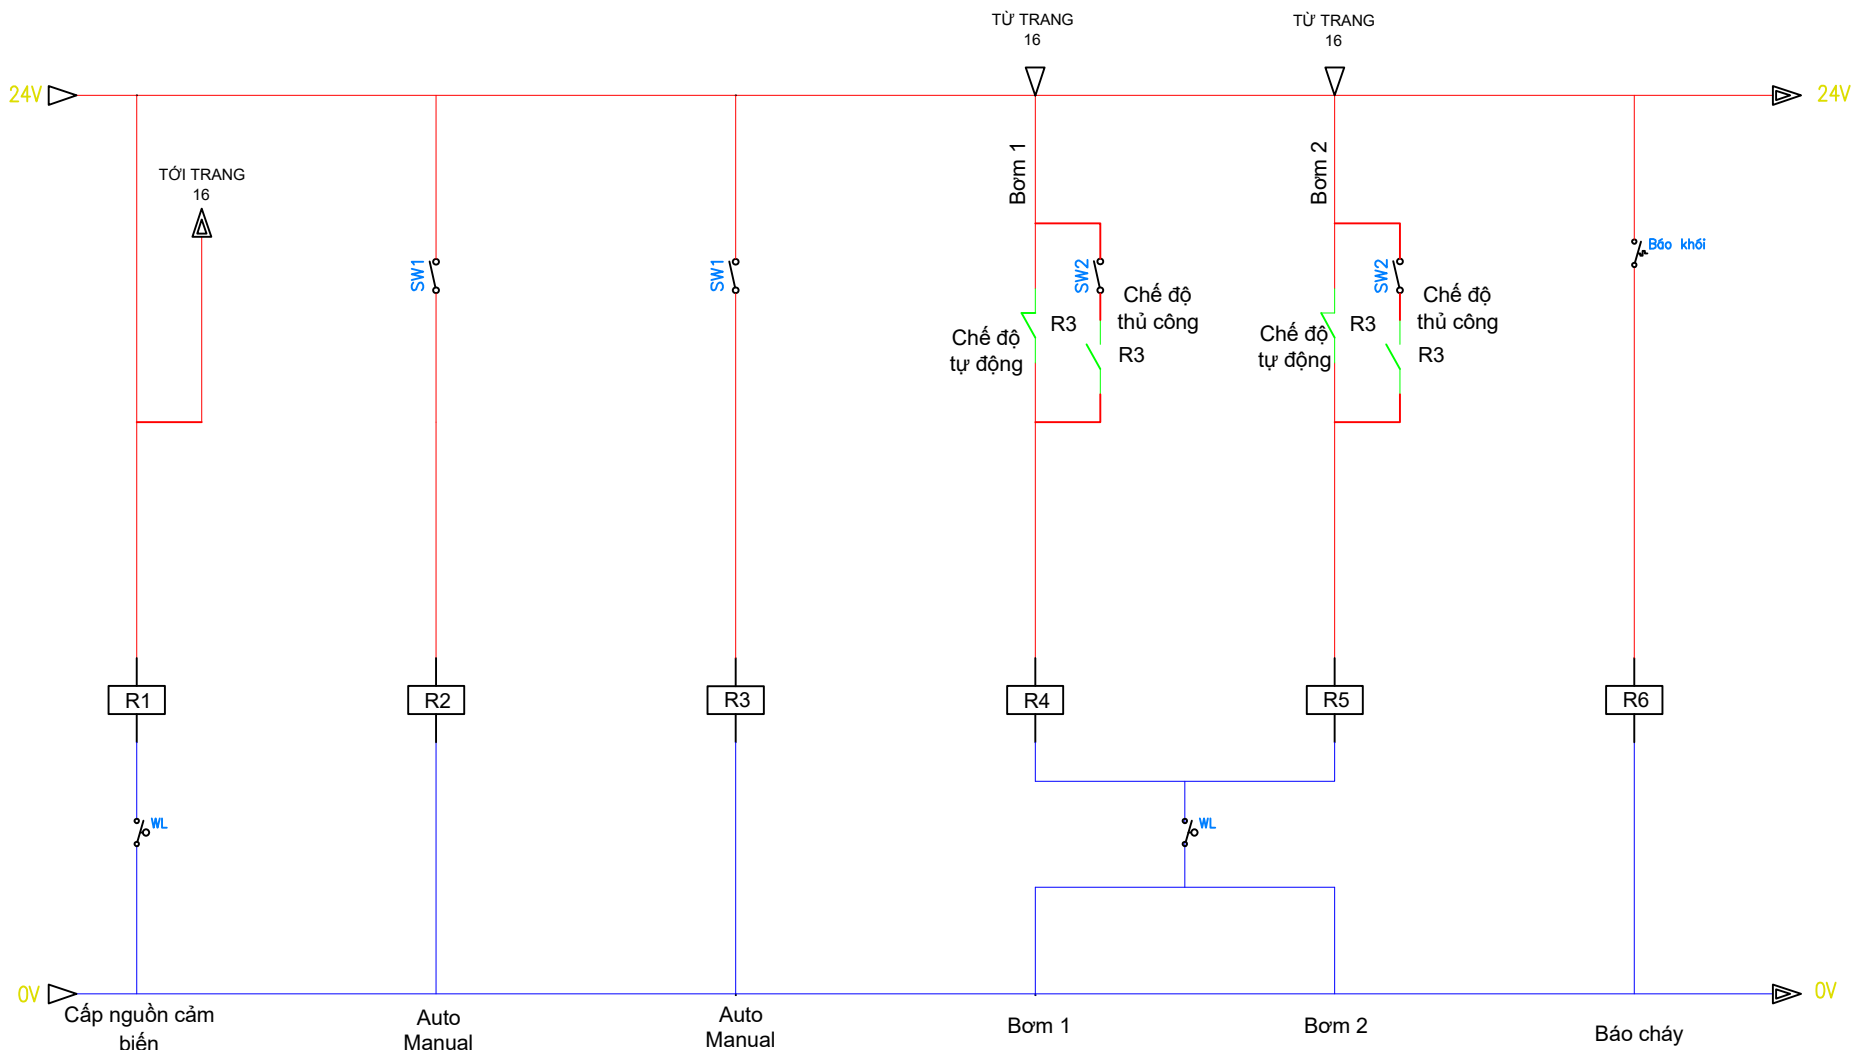

BẢN QUYỀN:

THIẾT KẾ VÀ BẢN IN NÀY LÀ TÀI SẢN CỦA
CÔNG TY SAIGON VALVE . KHÔNG ĐƯỢC SỬ
DỤNG, SAO CHÉP TOÀN BỘ HOẶC MỘT PHẦN
NẾU KHÔNG CÓ SỰ CHO PHÉP BẰNG VĂN BẢN
CỦA CÔNG TY



SAIGON VALVE COMPANY LIMITED
124/16-18 Võ Văn Hát, P.Long Trường, TP.Thủ Đức
PH : 028 8353 8739
Fax : 0316929581
Website : <https://saigonvalve.vn/>

DỰ ÁN : QUAN TRẮC CHẤT LƯỢNG
NƯỚC - NƯỚC SẠCH HUẾ

TIÊU ĐỀ : SƠ ĐỒ ĐIỀU KHIỂN

MÃ BẢN VẼ
DWG 1-10

PHIÊN BẢN
A

TRANG
11

TỈ LỆ
1/10

DỰ ÁN
1

NGÀY

...

NGƯỜI THIẾT KẾ


CHÂU VƯƠNG PHÁT

NGƯỜI KIỂM DUYỆT

NGUYỄN THÀNH NAM

NGƯỜI PHÊ DUYỆT

LÊ VĂN VĨNH

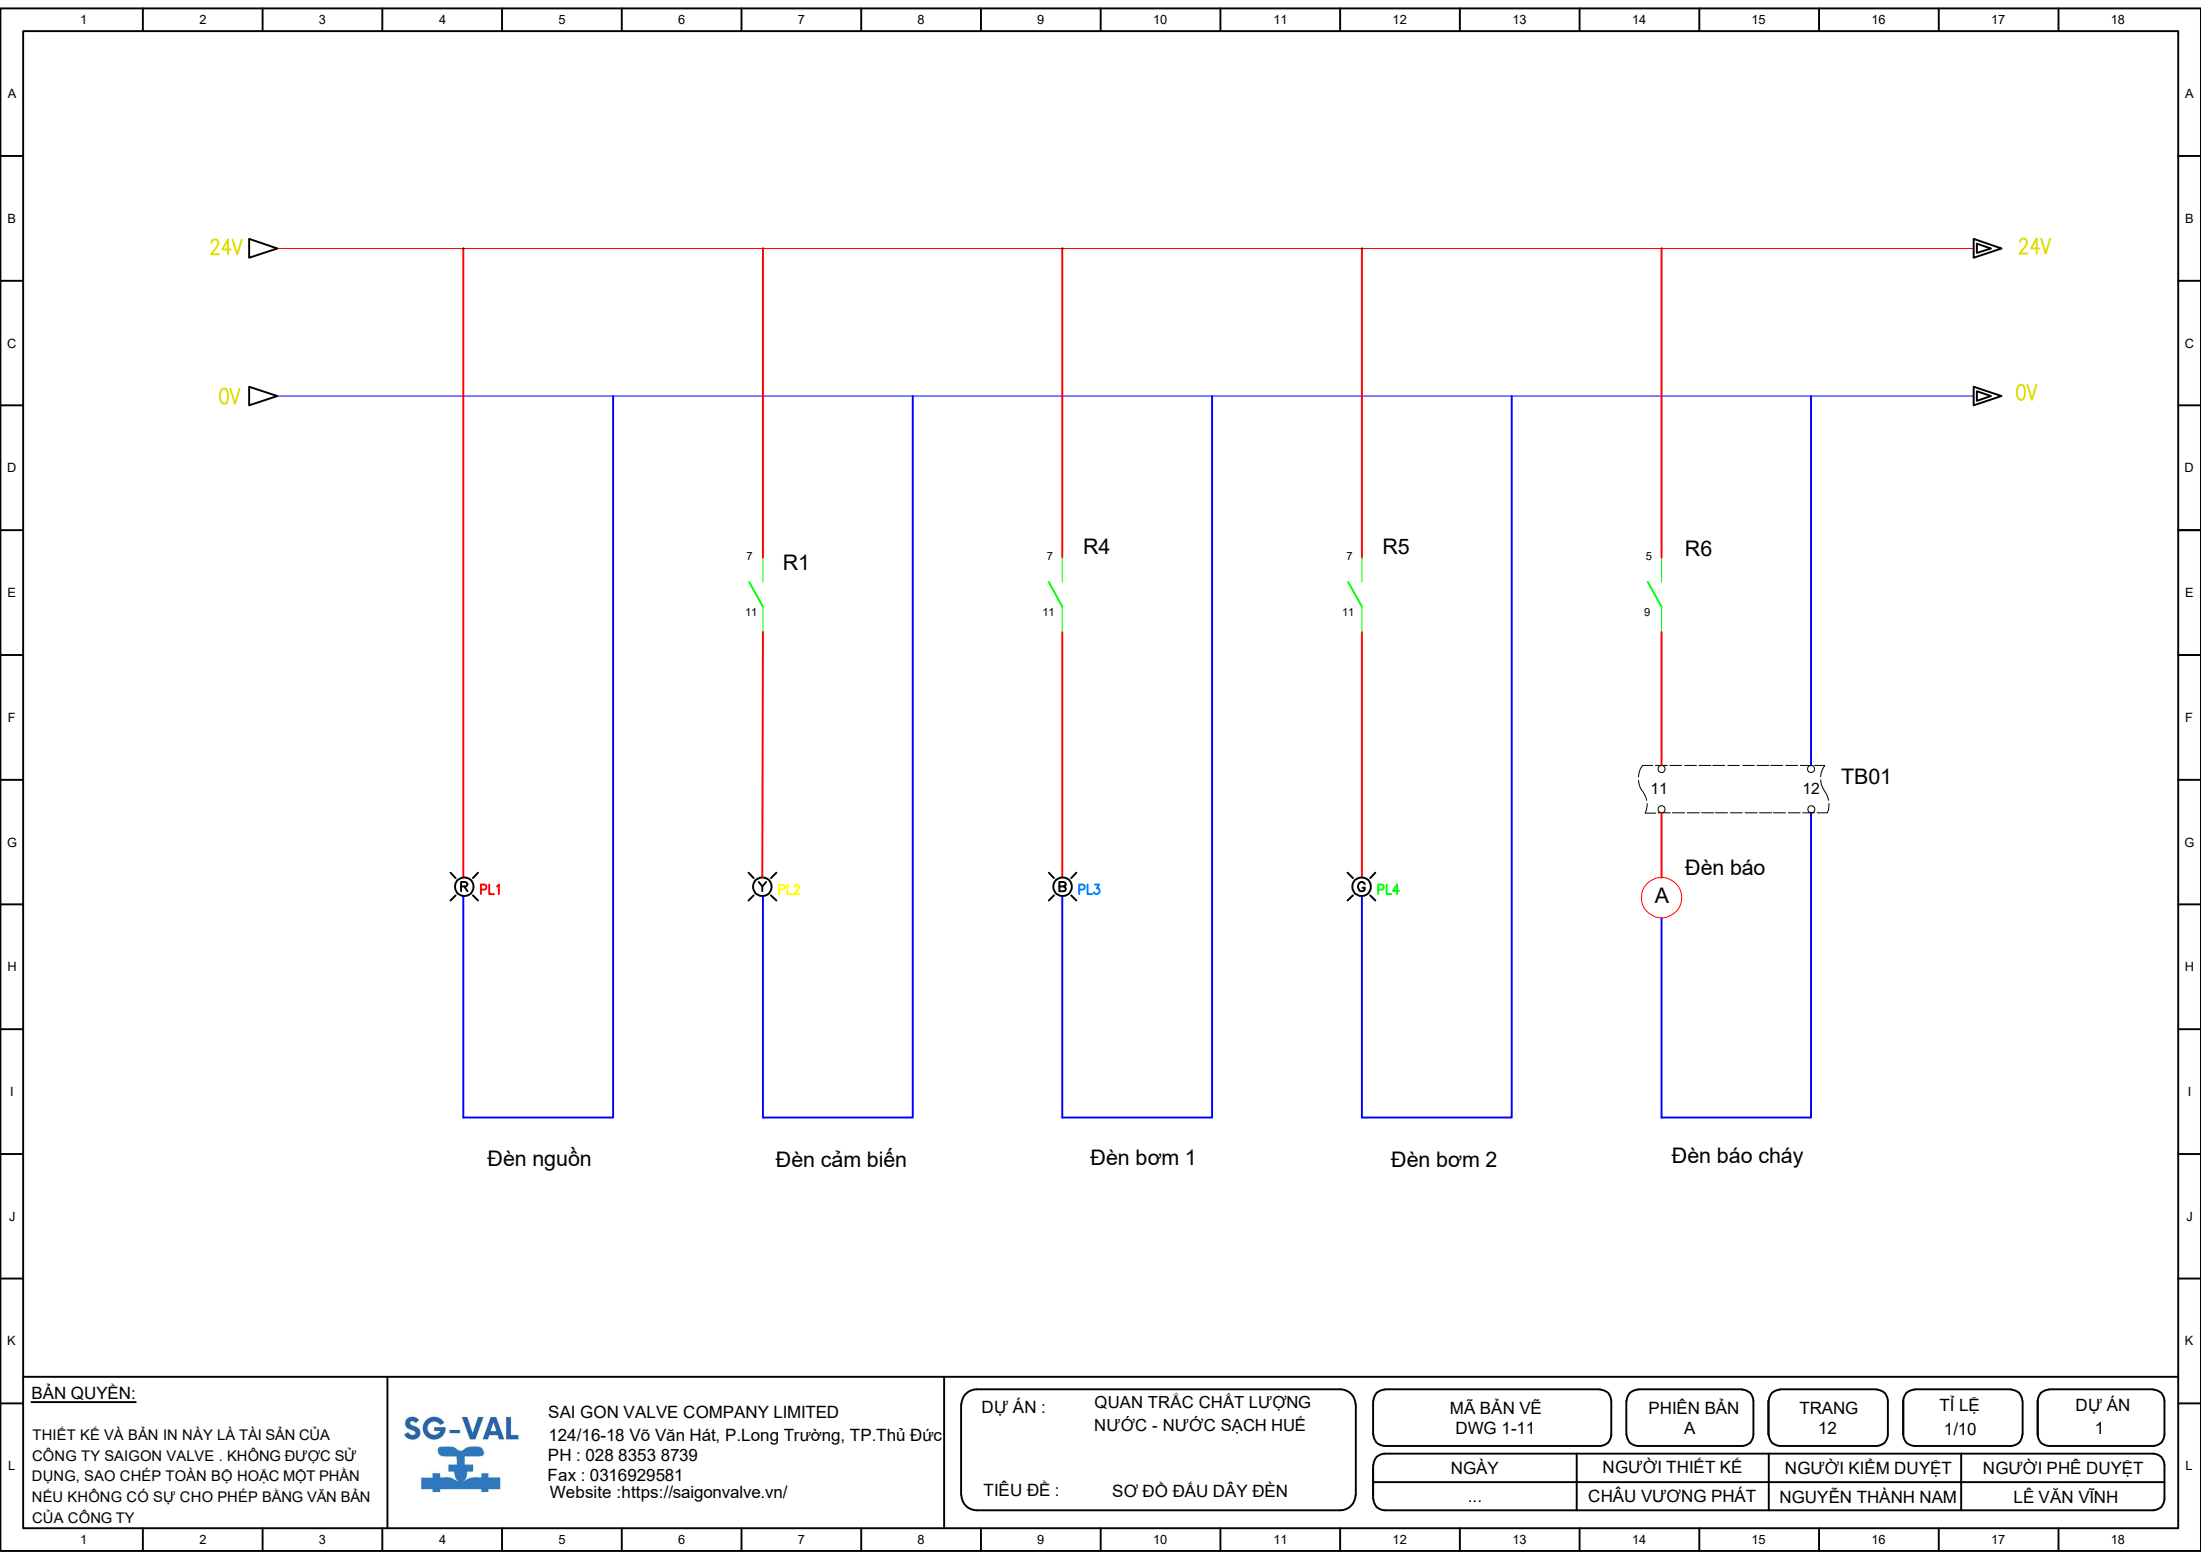

BẢN QUYỀN:

THIẾT KẾ VÀ BẢN IN NÀY LÀ TÀI SẢN CỦA
CÔNG TY SAIGON VALVE . KHÔNG ĐƯỢC SỬ
DỤNG, SAO CHÉP TOÀN BỘ HOẶC MỘT PHẦN
NẾU KHÔNG CÓ SỰ CHO PHÉP BẰNG VĂN BẢN
CỦA CÔNG TY



SAI GON VALVE COMPANY LIMITED
124/16-18 Võ Văn Hát, P.Long Trường, TP.Thủ Đức
PH : 028 8353 8739
Fax : 0316929581
Website :<https://saigonvalve.vn/>

DỰ ÁN : QUAN TRẮC CHẤT LƯỢNG
 NƯỚC - NƯỚC SẠCH HUẾ

TIÊU ĐỀ : SƠ ĐỒ ĐẦU DÂY ĐÈN

MÃ BẢN VẼ
DWG 1-11

PHIÊN BẢN
A

TRANG
12

TỈ LỆ
1/10

DỰ ÁN
1

NGÀY

NGƯỜI THIẾT KẾ

NGƯỜI KIỂM DUYỆT

NGƯỜI PHÊ DUYỆT


...

CHÂU VƯƠNG PHÁT


NGUYỄN THÀNH NAM

LÊ VĂN VĨNH

THỦ CÔNG

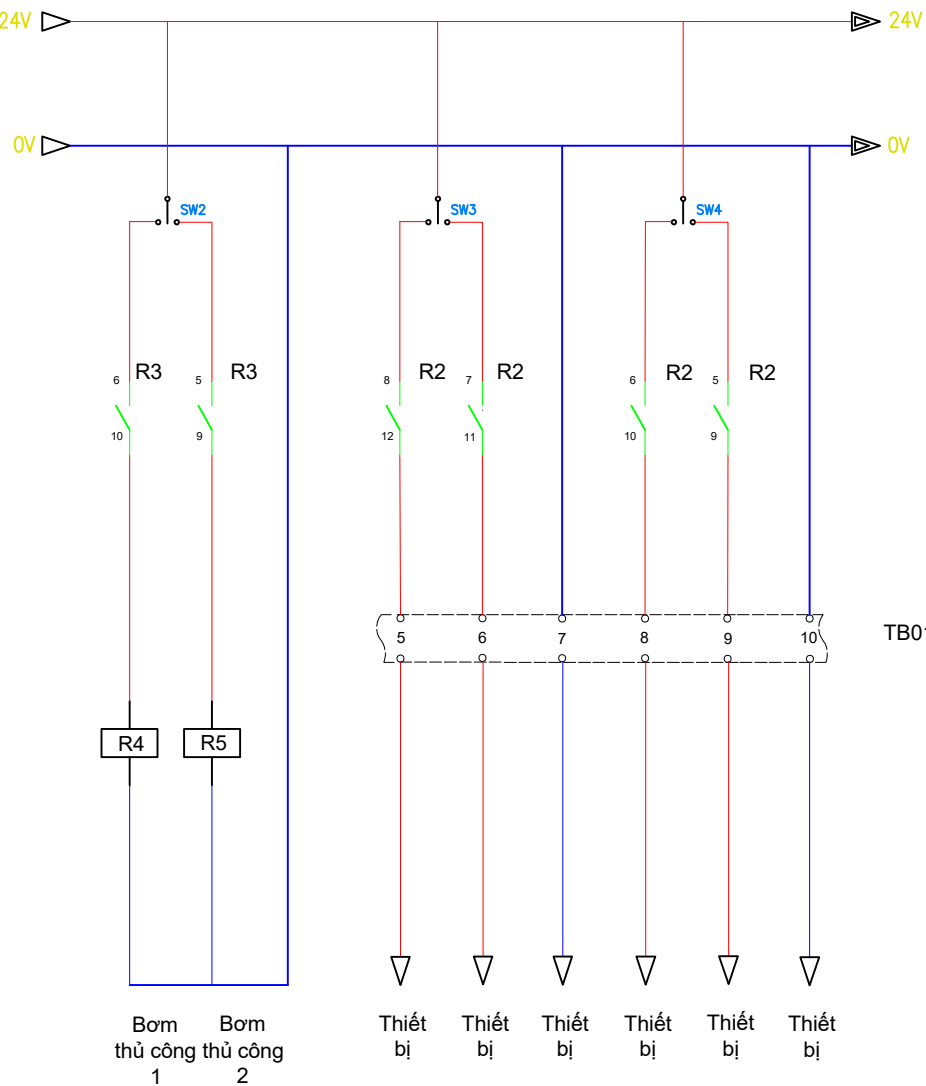

TỰ ĐỘNG

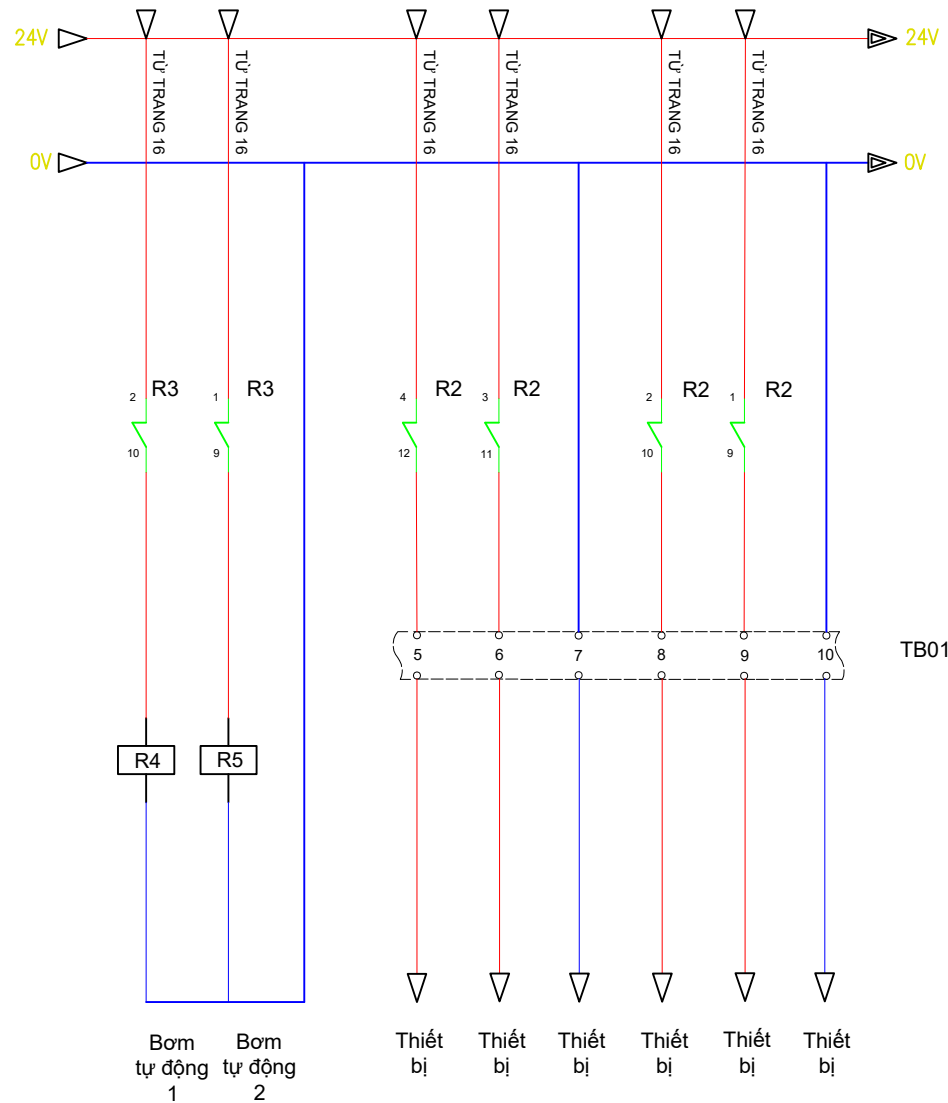

BẢN QUYỀN:

THIẾT KẾ VÀ BẢN IN NÀY LÀ TÀI SẢN CỦA CÔNG TY SAIGON VALVE. KHÔNG ĐƯỢC SỬ DỤNG, SAO CHÉP TOÀN BỘ HOẶC MỘT PHẦN NẾU KHÔNG CÓ SỰ CHO PHÉP BẰNG VĂN BẢN CỦA CÔNG TY



SAIGON VALVE COMPANY LIMITED
124/16-18 Võ Văn Hát, P.Long Trường, TP.Thủ Đức
PH : 028 8353 8739
Fax : 0316929581
Website : <https://saigonvalve.vn/>

DỰ ÁN : QUAN TRẮC CHẤT LƯỢNG NƯỚC - NƯỚC SẠCH HUẾ

TIÊU ĐỀ : CHẾ ĐỘ TỰ ĐỘNG/ THỦ CÔNG

MÃ BẢN VẼ
DWG 1-12

PHIÊN BẢN
A

TRANG
13

TỈ LỆ
1/10

DỰ ÁN
1

NGÀY

...

NGƯỜI THIẾT KẾ


CHÂU VƯƠNG PHÁT

NGƯỜI KIỂM DUYỆT

NGUYỄN THÀNH NAM

NGƯỜI PHÊ DUYỆT

LÊ VĂN VĨNH

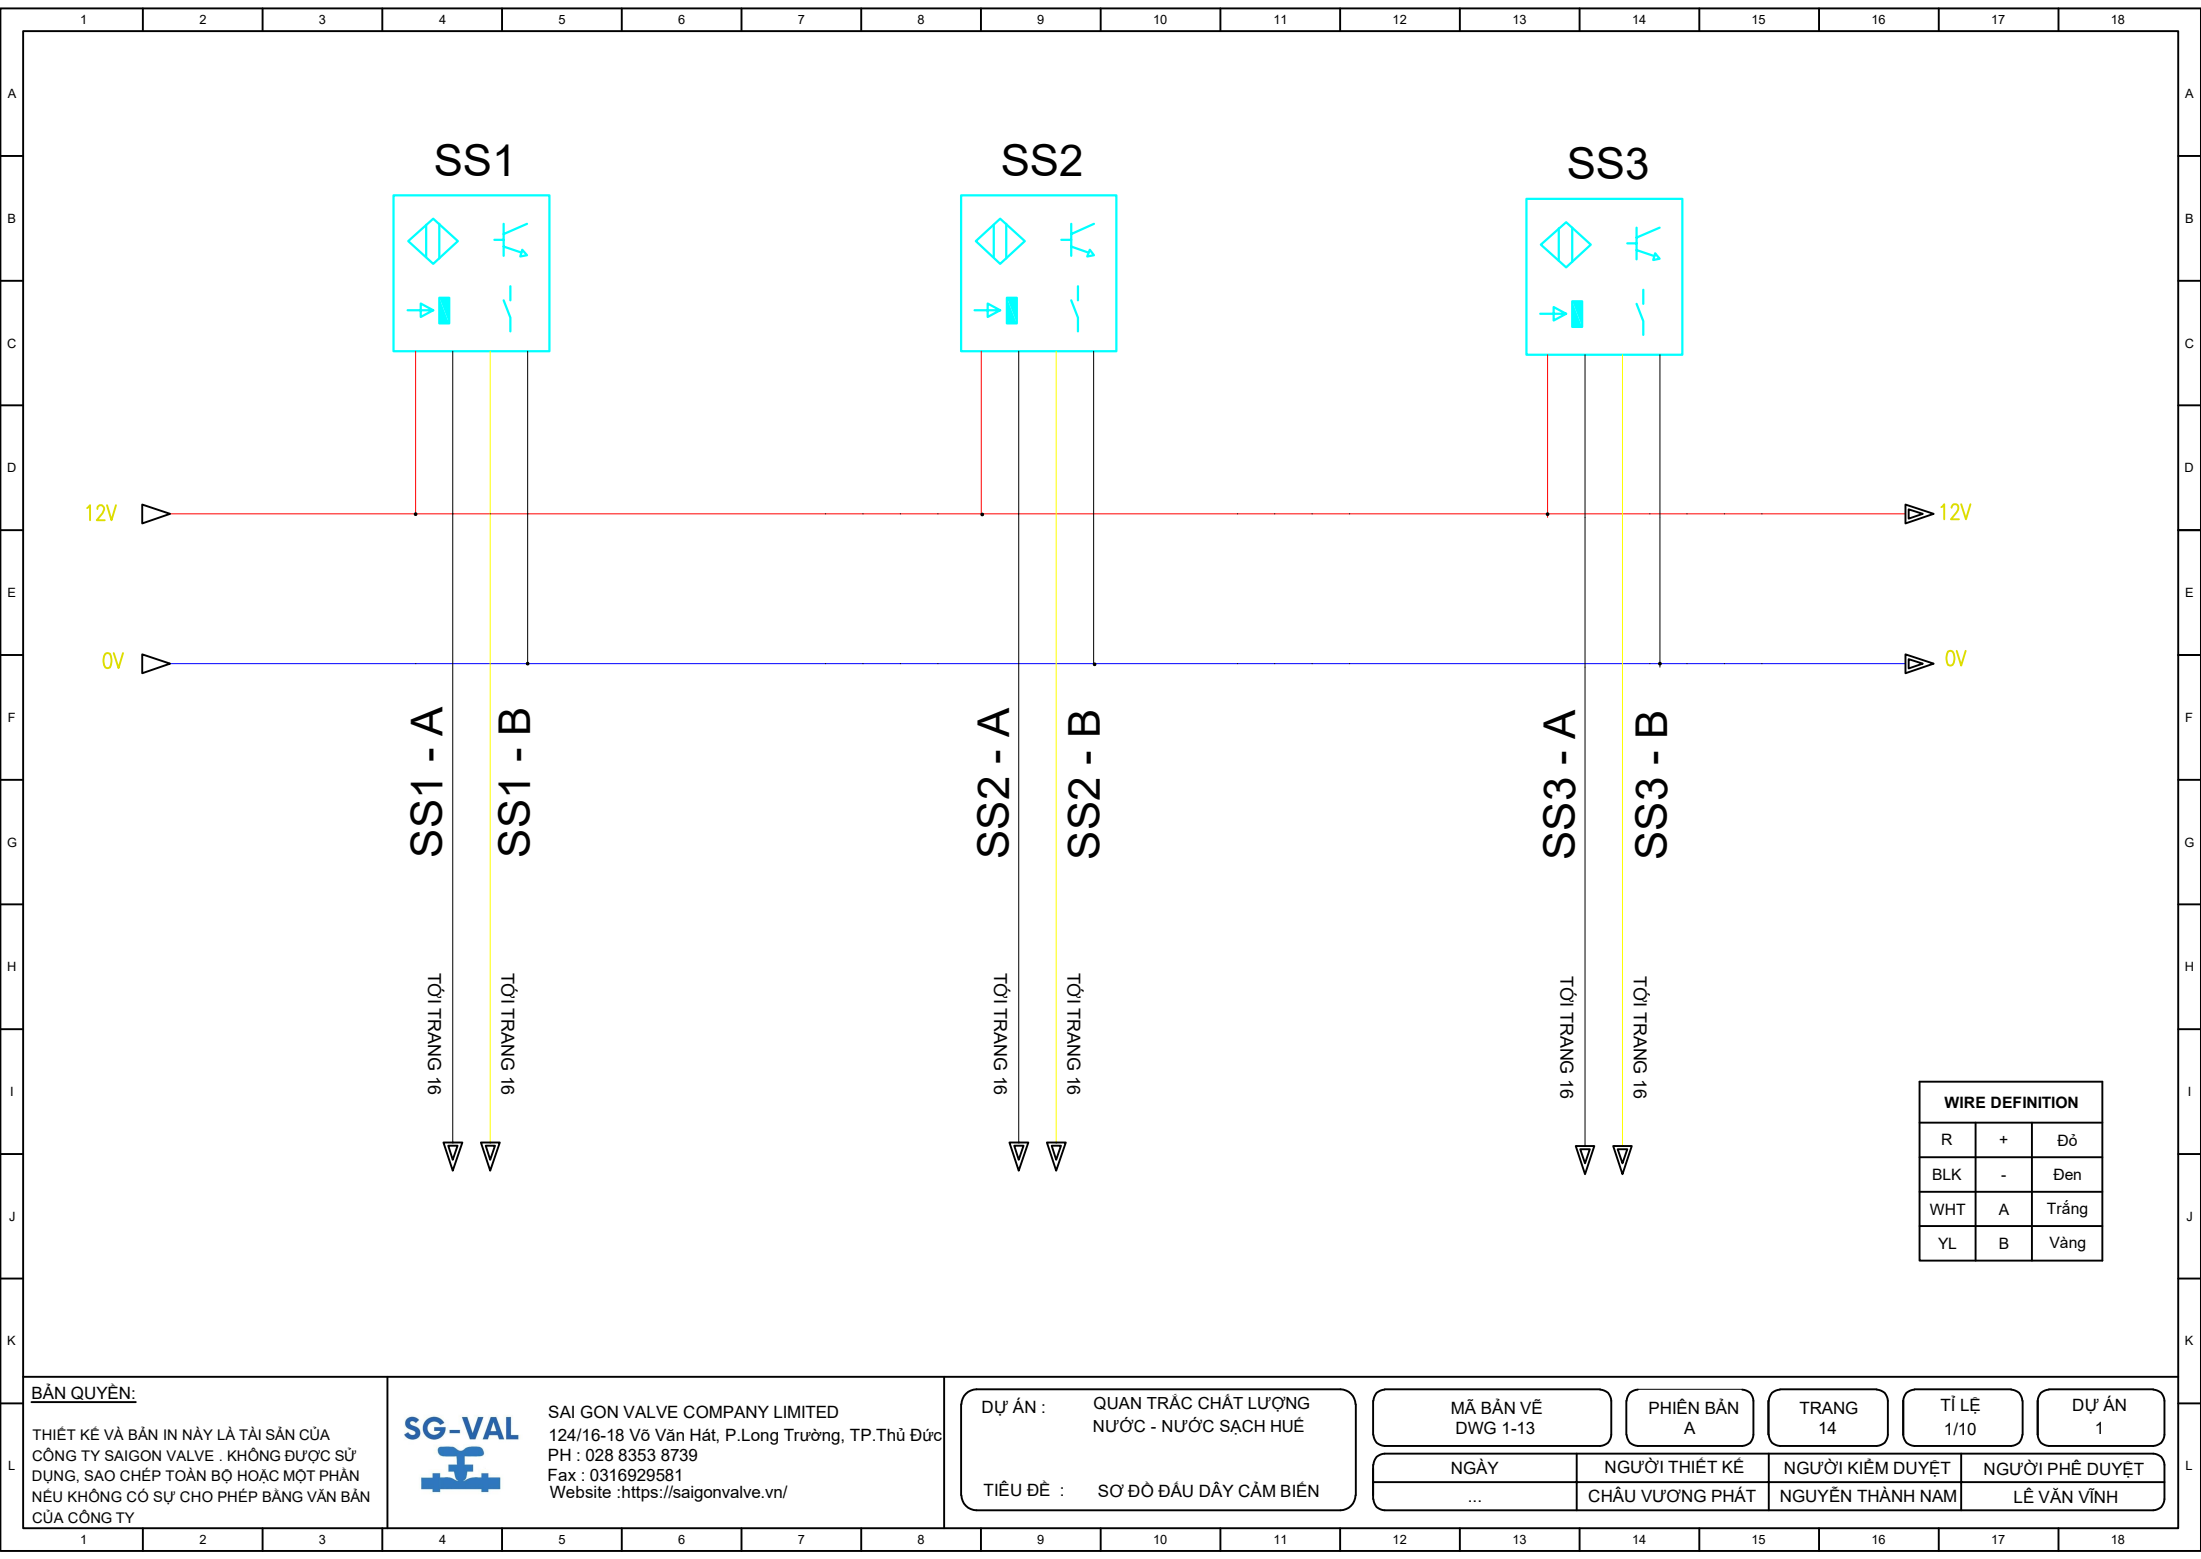

WIRE DEFINITION		
R	+	Đỏ
BLK	-	Đen
WHT	A	Trắng
YL	B	Vàng

BẢN QUYỀN:

THIẾT KẾ VÀ BẢN IN NÀY LÀ TÀI SẢN CỦA
CÔNG TY SAIGON VALVE . KHÔNG ĐƯỢC SỬ
DỤNG, SAO CHÉP TOÀN BỘ HOẶC MỘT PHẦN
NẾU KHÔNG CÓ SỰ CHO PHÉP BẰNG VĂN BẢN
CỦA CÔNG TY



SAI GON VALVE COMPANY LIMITED
124/16-18 Võ Văn Hát, P.Long Trường, TP.Thủ Đức
PH : 028 8353 8739
Fax : 0316929581
Website : <https://saigonvalve.vn/>

DỰ ÁN : QUAN TRẮC CHẤT LƯỢNG
NƯỚC - NƯỚC SẠCH HUẾ

TIÊU ĐỀ : SƠ ĐỒ ĐẦU DÂY CẢM BIẾN

MÃ BẢN VẼ
DWG 1-13

PHIÊN BẢN
A

TRANG
14

TỈ LỆ
1/10

DỰ ÁN
1

NGÀY

...

NGƯỜI THIẾT KẾ


CHÂU VƯƠNG PHÁT

NGƯỜI KIỂM DUYỆT

NGUYỄN THÀNH NAM

NGƯỜI PHÊ DUYỆT

LÊ VĂN VĨNH

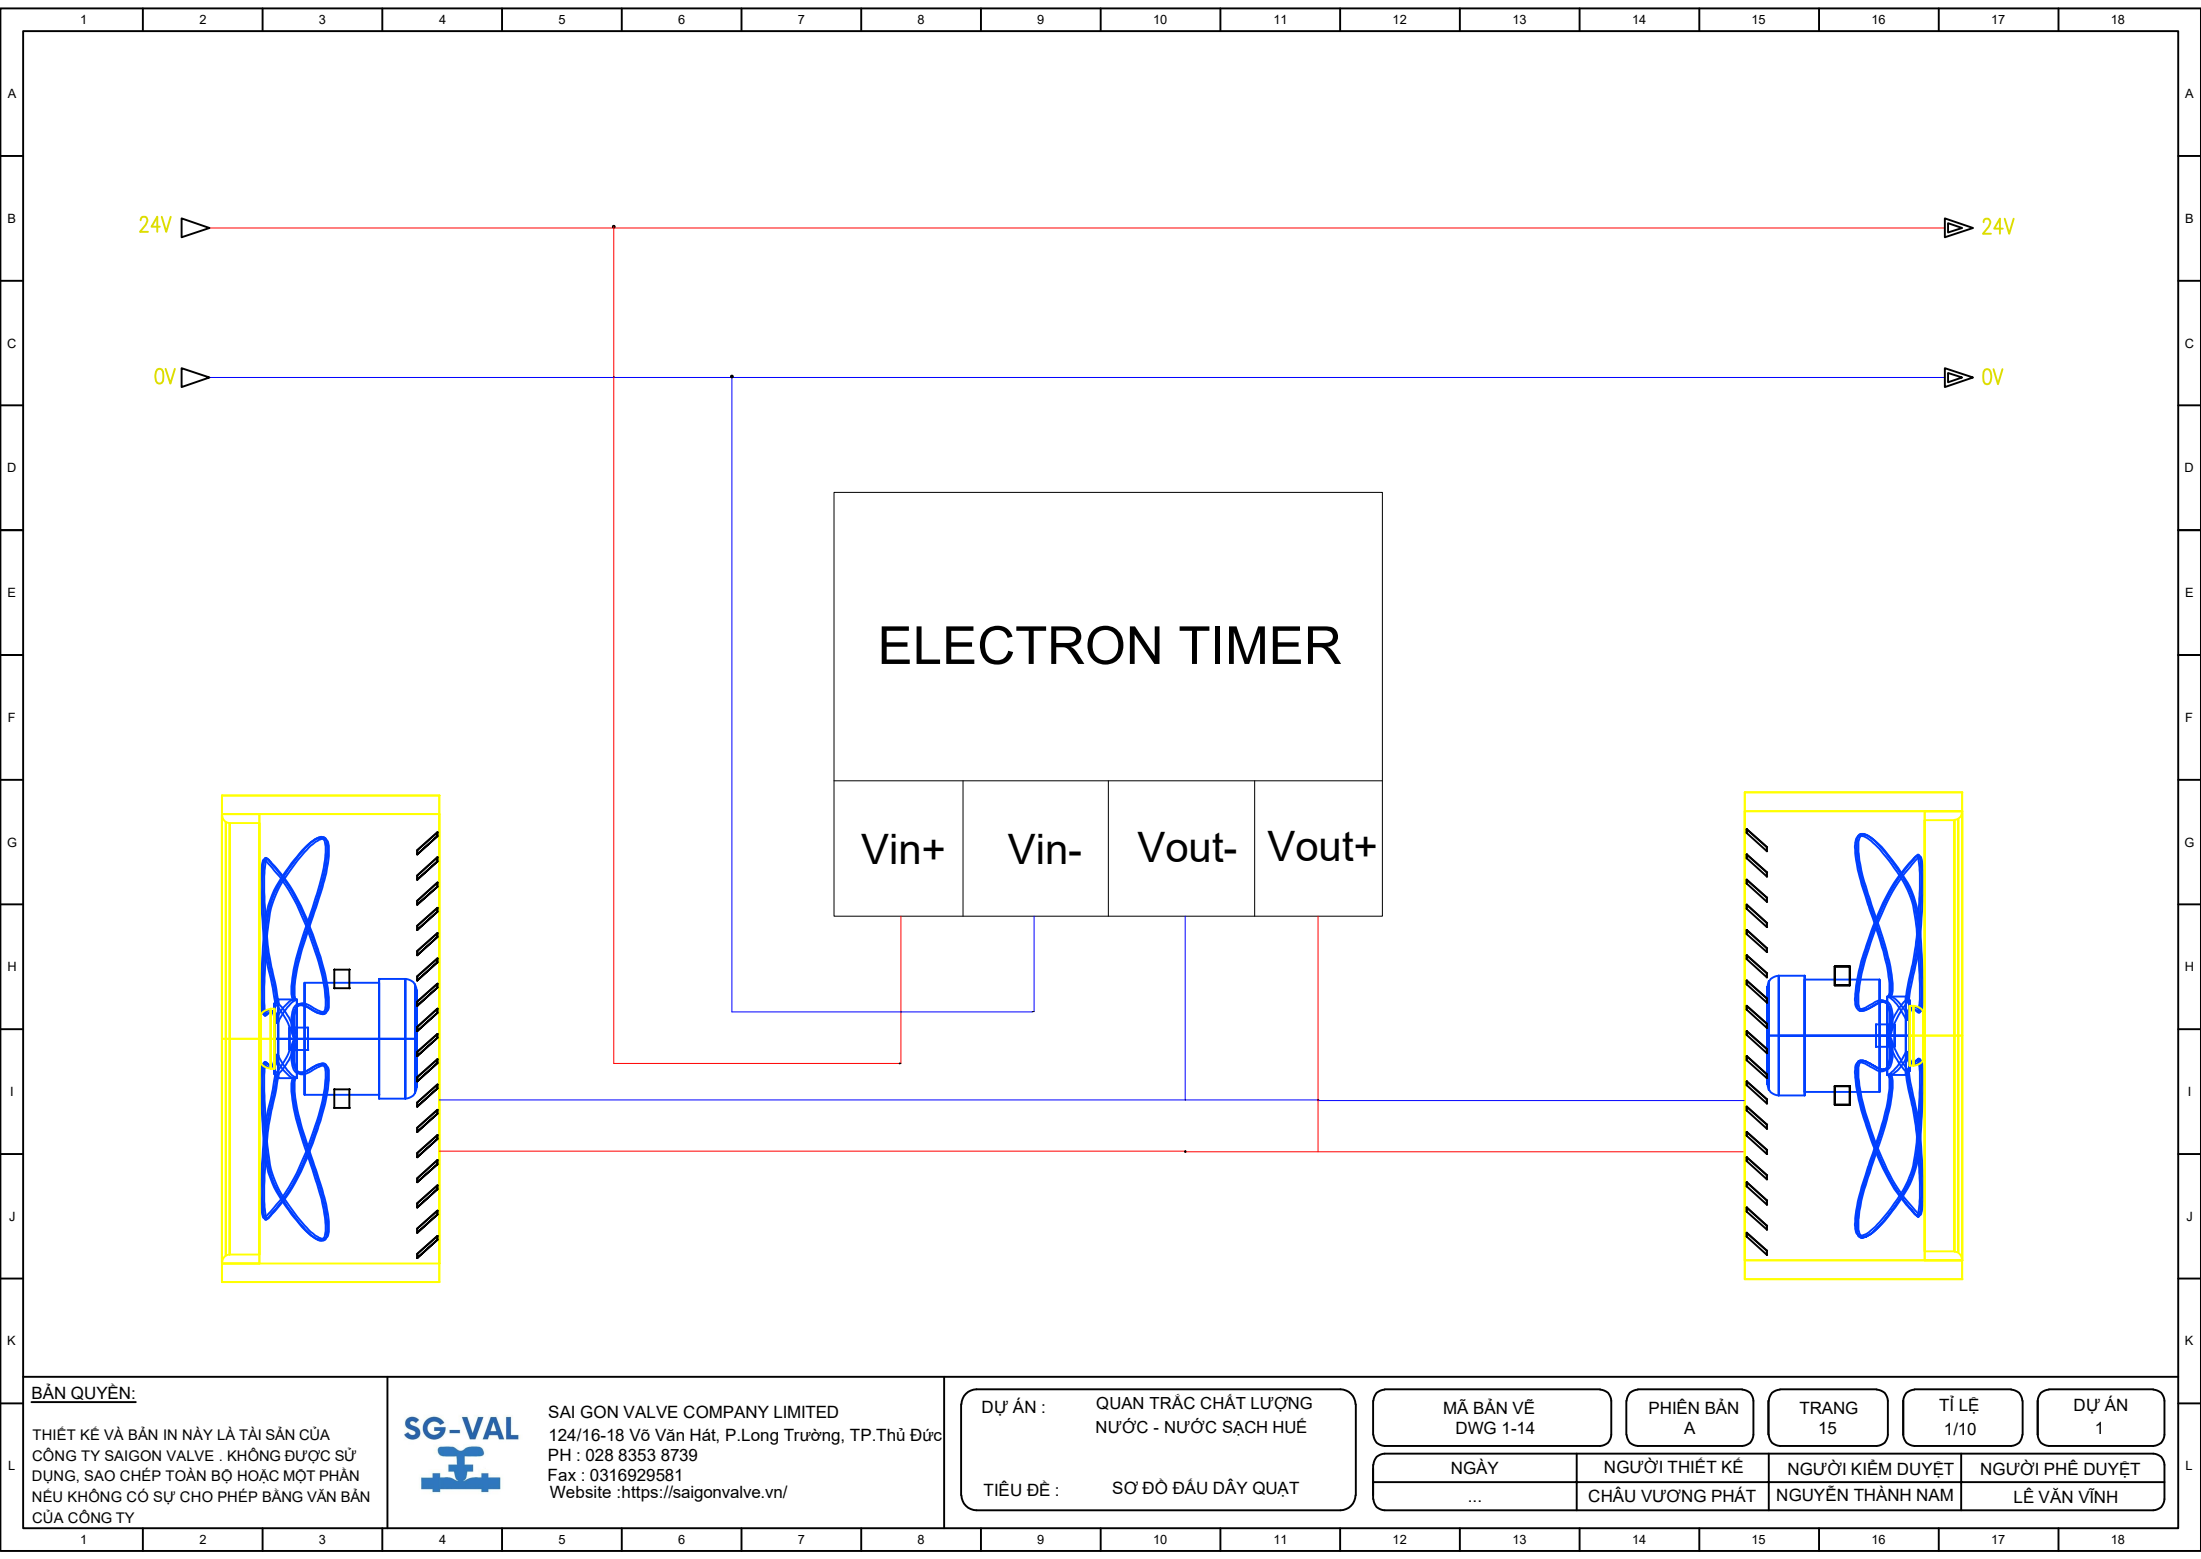

BẢN QUYỀN:


THIẾT KẾ VÀ BẢN IN NÀY LÀ TÀI SẢN CỦA
CÔNG TY SAIGON VALVE . KHÔNG ĐƯỢC SỬ
DỤNG, SAO CHÉP TOÀN BỘ HOẶC MỘT PHẦN
NẾU KHÔNG CÓ SỰ CHO PHÉP BẰNG VĂN BẢN
CỦA CÔNG TY



SAI GON VALVE COMPANY LIMITED
124/16-18 Võ Văn Hát, P.Long Trường, TP.Thủ Đức
PH : 028 8353 8739
Fax : 0316929581
Website : <https://saigonvalve.vn/>

DỰ ÁN : QUAN TRẮC CHẤT LƯỢNG
NƯỚC - NƯỚC SẠCH HUẾ
TIÊU ĐỀ : SƠ ĐỒ ĐẦU DÂY QUẠT

MÃ BẢN VẼ DWG 1-14	PHIÊN BẢN A	TRANG 15	TỈ LỆ 1/10	DỰ ÁN 1
NGÀY ...	NGƯỜI THIẾT KẾ CHÂU VƯƠNG PHÁT	NGƯỜI KIỂM DUYỆT NGUYỄN THÀNH NAM	NGƯỜI PHÊ DUYỆT LÊ VĂN VĨNH	

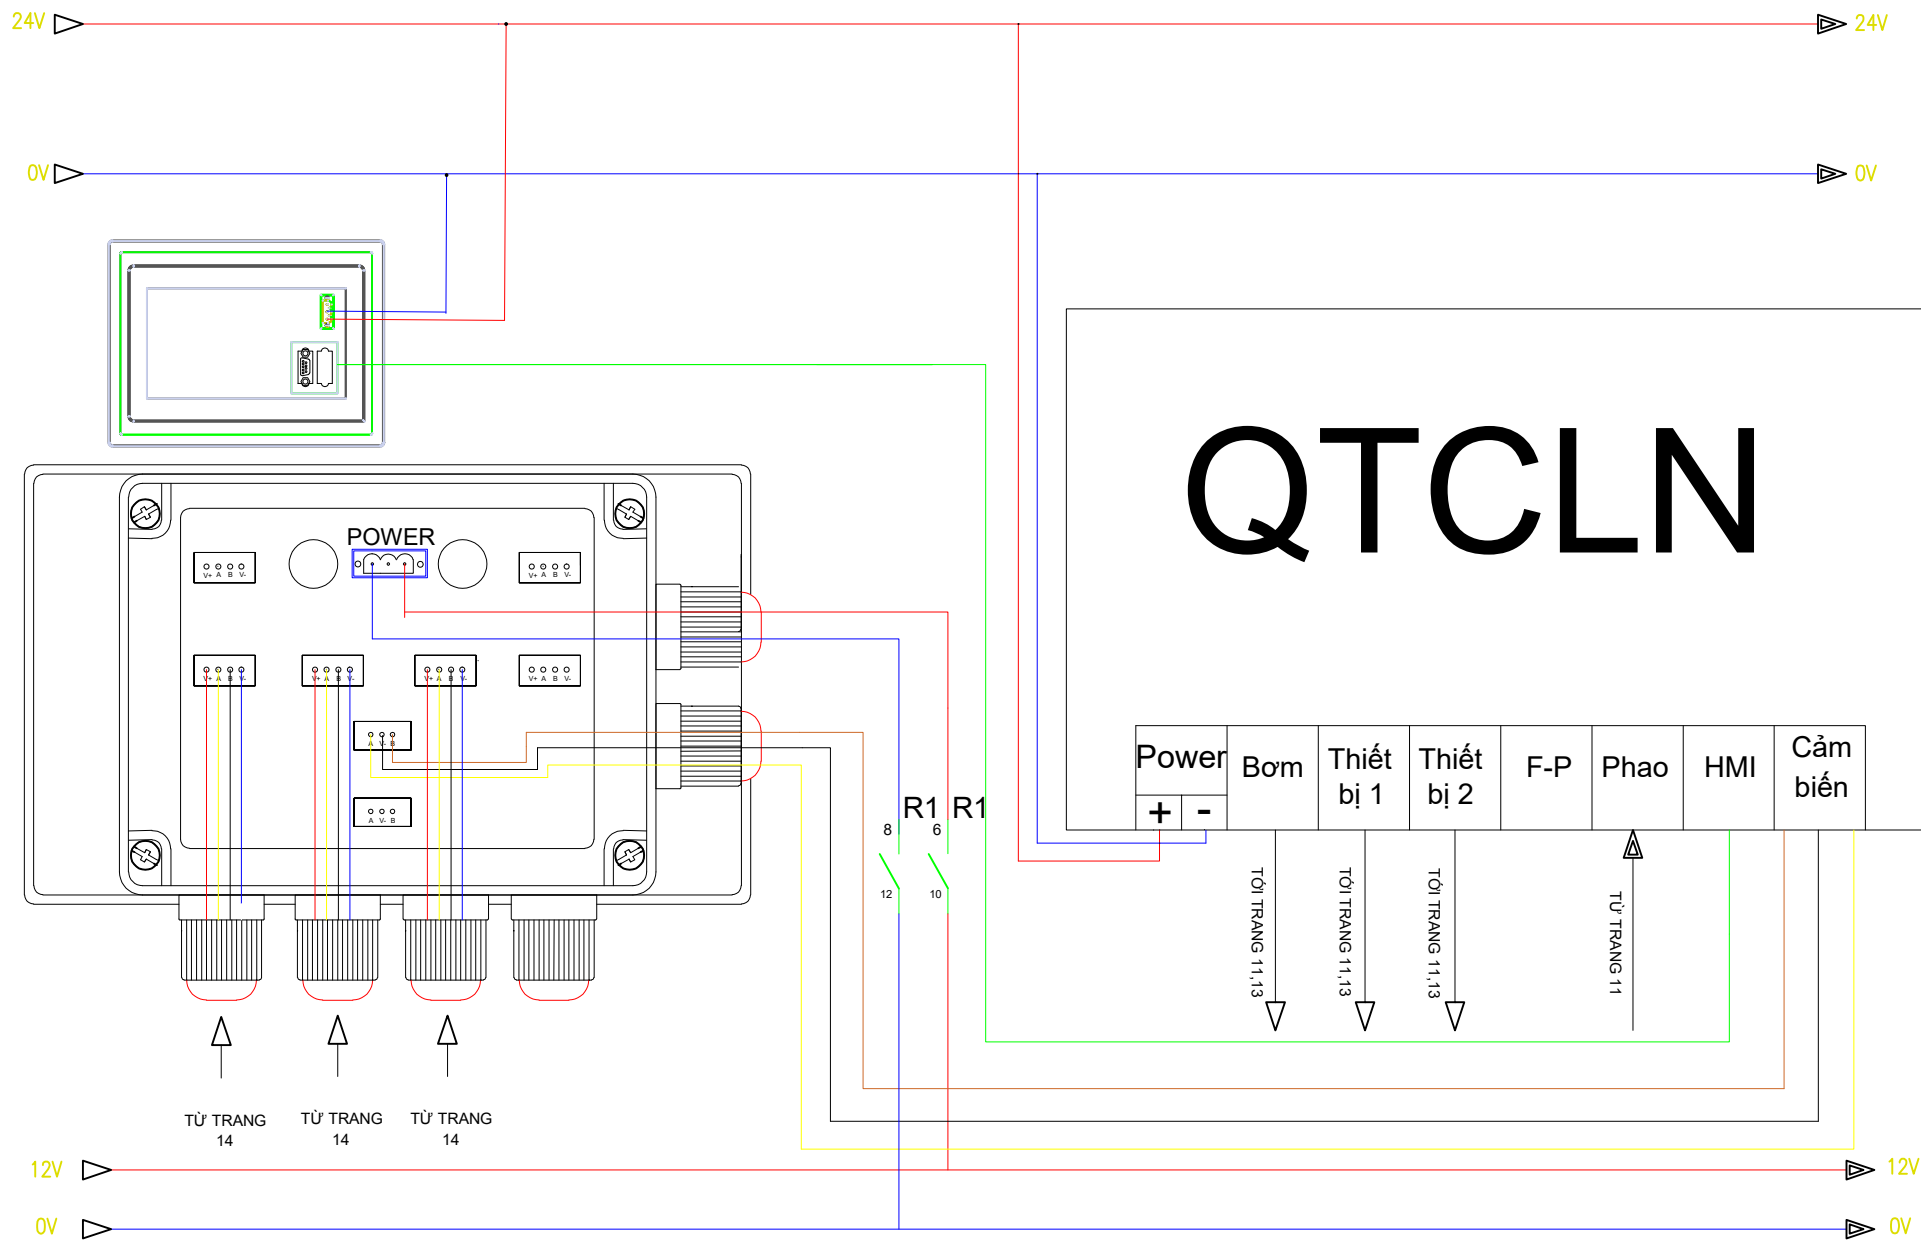

QTCNL

Power	Bơm	Thiết bị 1	Thiết bị 2	F-P	Phao	HMI	Cảm biến
+	TỐI TRẮNG 11,13	TỐI TRẮNG 11,13	TỐI TRẮNG 11,13	TỐI TRẮNG 11			
-							

BẢN QUYỀN:

THIẾT KẾ VÀ BẢN IN NÀY LÀ TÀI SẢN CỦA CÔNG TY SAIGON VALVE. KHÔNG ĐƯỢC SỬ DỤNG, SAO CHÉP TOÀN BỘ HOẶC MỘT PHẦN NẾU KHÔNG CÓ SỰ CHO PHÉP BẰNG VĂN BẢN CỦA CÔNG TY



SAIGON VALVE COMPANY LIMITED
124/16-18 Võ Văn Hát, P.Long Trường, TP.Thủ Đức
PH : 028 8353 8739
Fax : 0316929581
Website : <https://saigonvalve.vn/>

DỰ ÁN : QUAN TRẮC CHẤT LƯỢNG NƯỚC - NƯỚC SẠCH HUẾ

TIÊU ĐỀ : SƠ ĐỒ ĐẦU DÂY BỘ ĐIỀU KHIỂN

MÃ BẢN VẼ
DWG 1-15

PHIÊN BẢN
A

TRANG
16

TỈ LỆ
1/10

DỰ ÁN
1

NGÀY

...

NGƯỜI THIẾT KẾ

CHÂU VƯƠNG PHÁT

NGƯỜI KIỂM DUYỆT

NGUYỄN THÀNH NAM

NGƯỜI PHÊ DUYỆT

LÊ VĂN VĨNH